
Kurmanaly.com

INTERIOR DESIGN · BISHKEK · MOSCOW

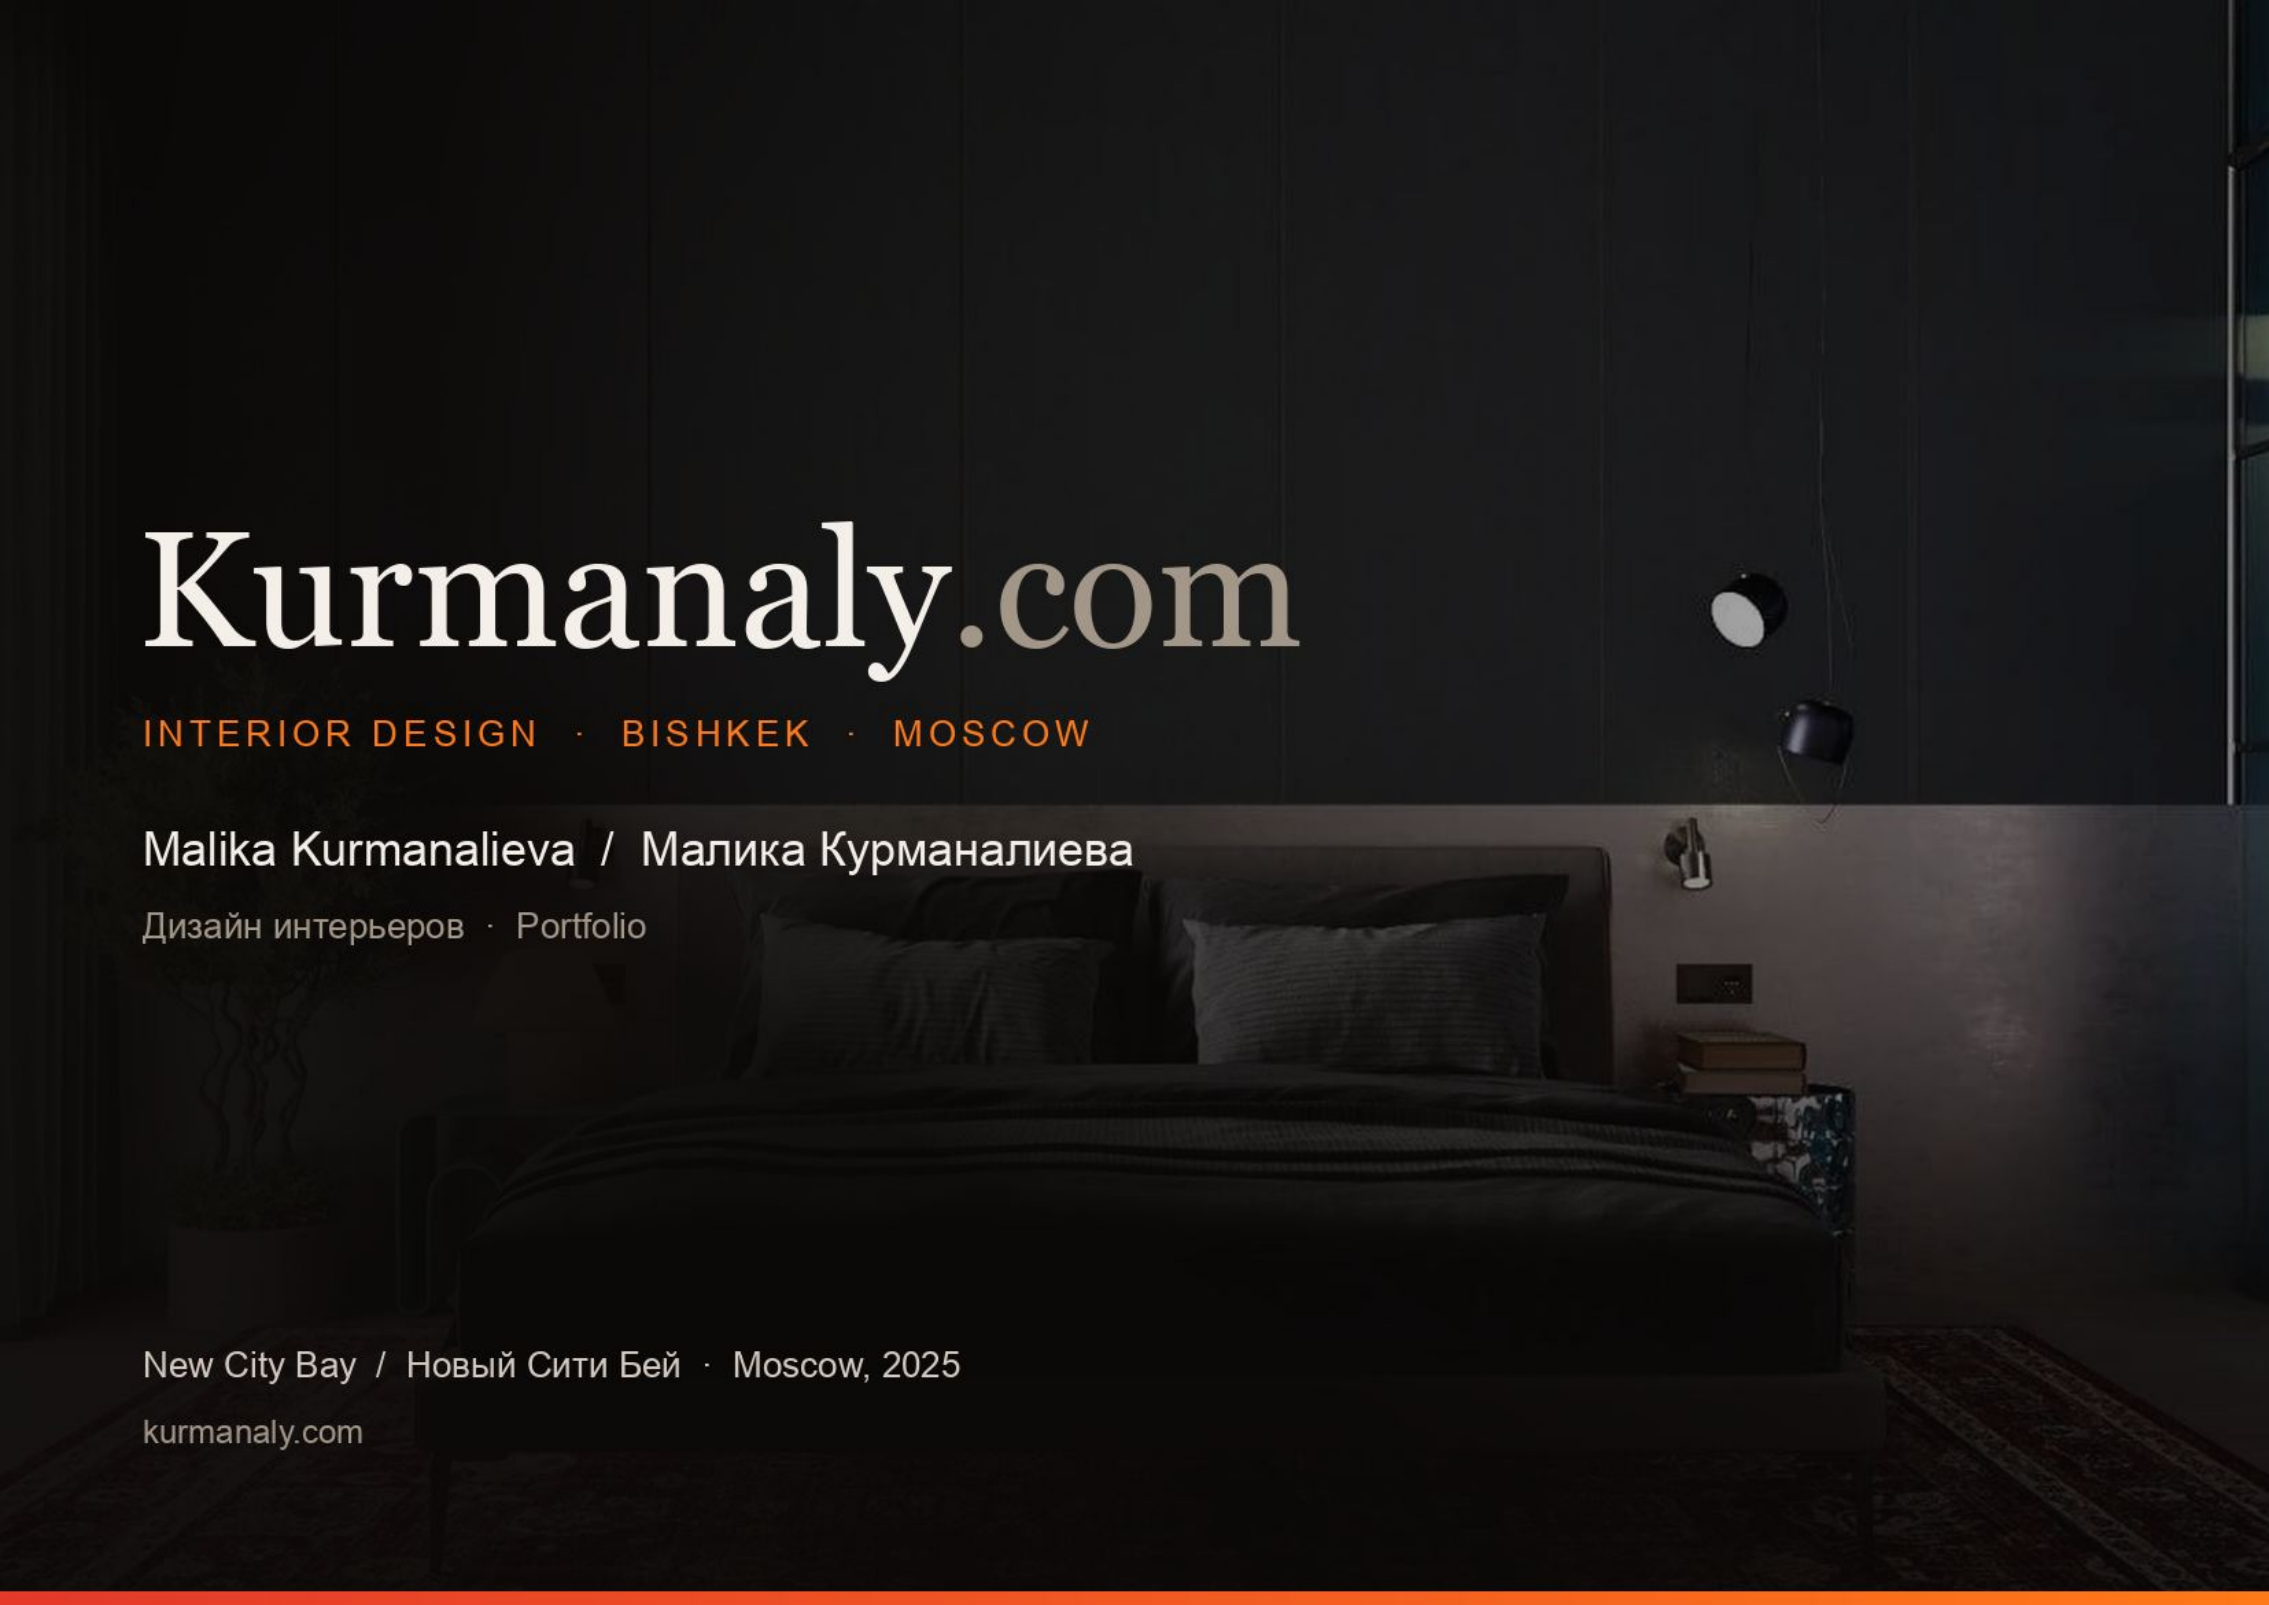

Malika Kurmanalieva / Малика Курманалиева

Дизайн интерьеров · Portfolio

New City Bay / Новый Сити Бей · Moscow, 2025

kurmanaly.com












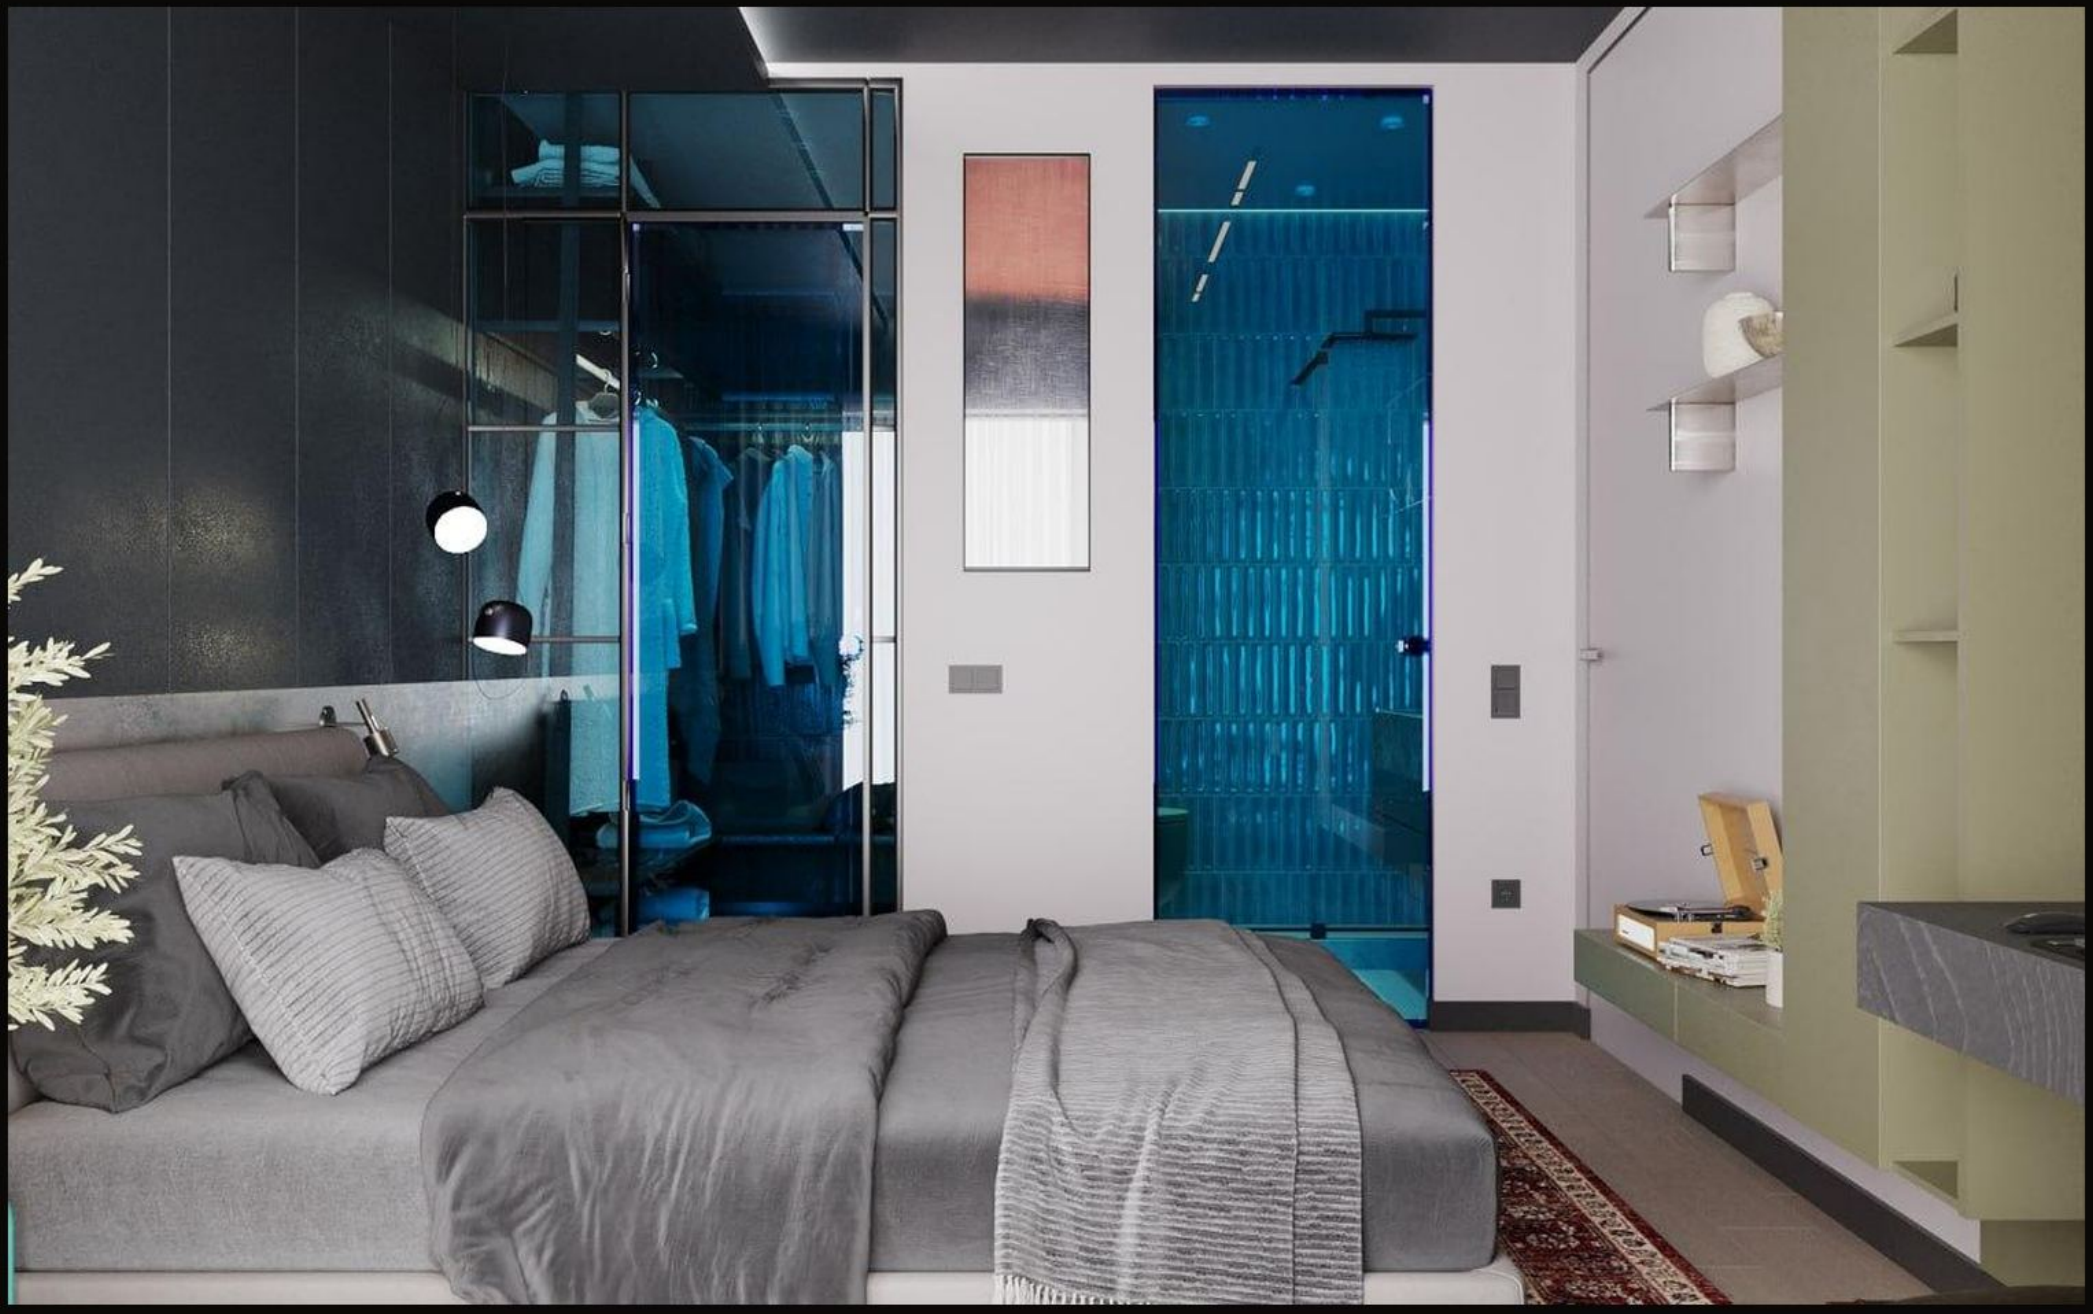















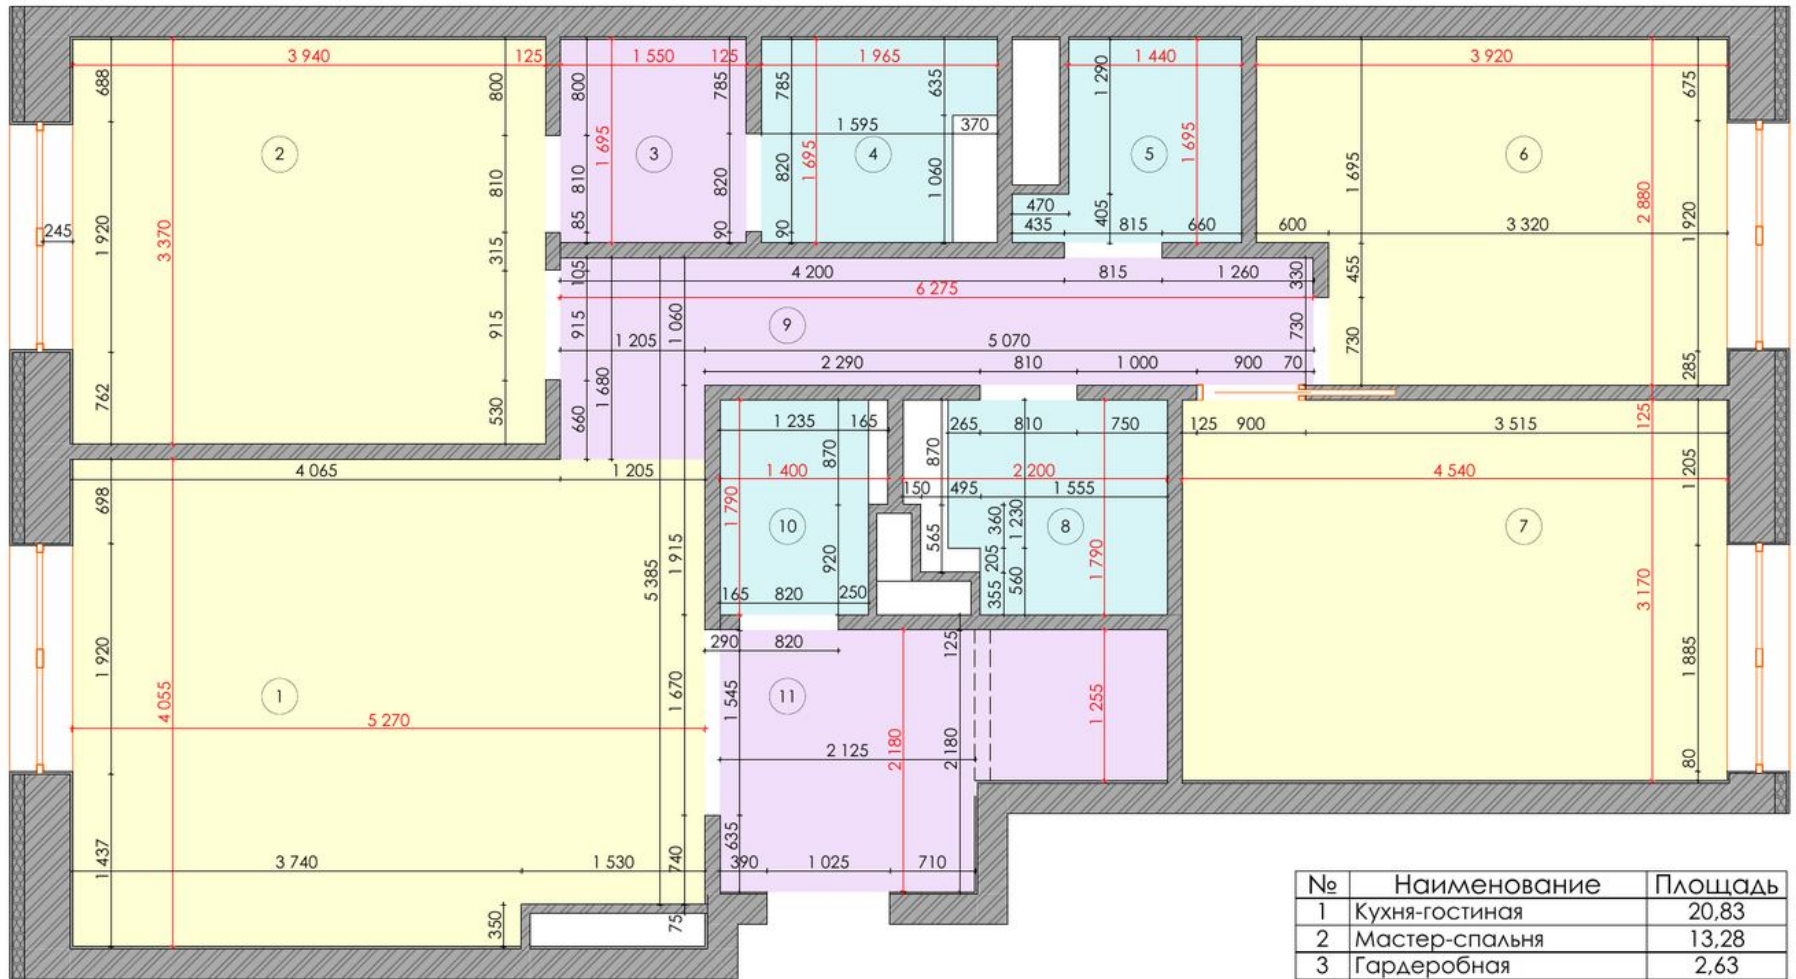

№	Наименование	Площадь
1	Кухня-гостиная	20,83
2	Мастер-спальня	13,28
3	Гардеробная	2,63
4	С/у	2,94
5	Постирочная	2,63
6	Комната	10,58
7	Комната	14,39
8	С/у	3,12
9	Коридор	7,40
10	С/у гостевой	2,21
11	Прихожая	6,64
		86,65 м²

Чертежник:	Курманалиева	Малика		г. Москва	Стадия	Лист	Листов
Визуализатор:	Маматибраимова	Амина			#Стадия Проекта	03	
				Обмерный план			

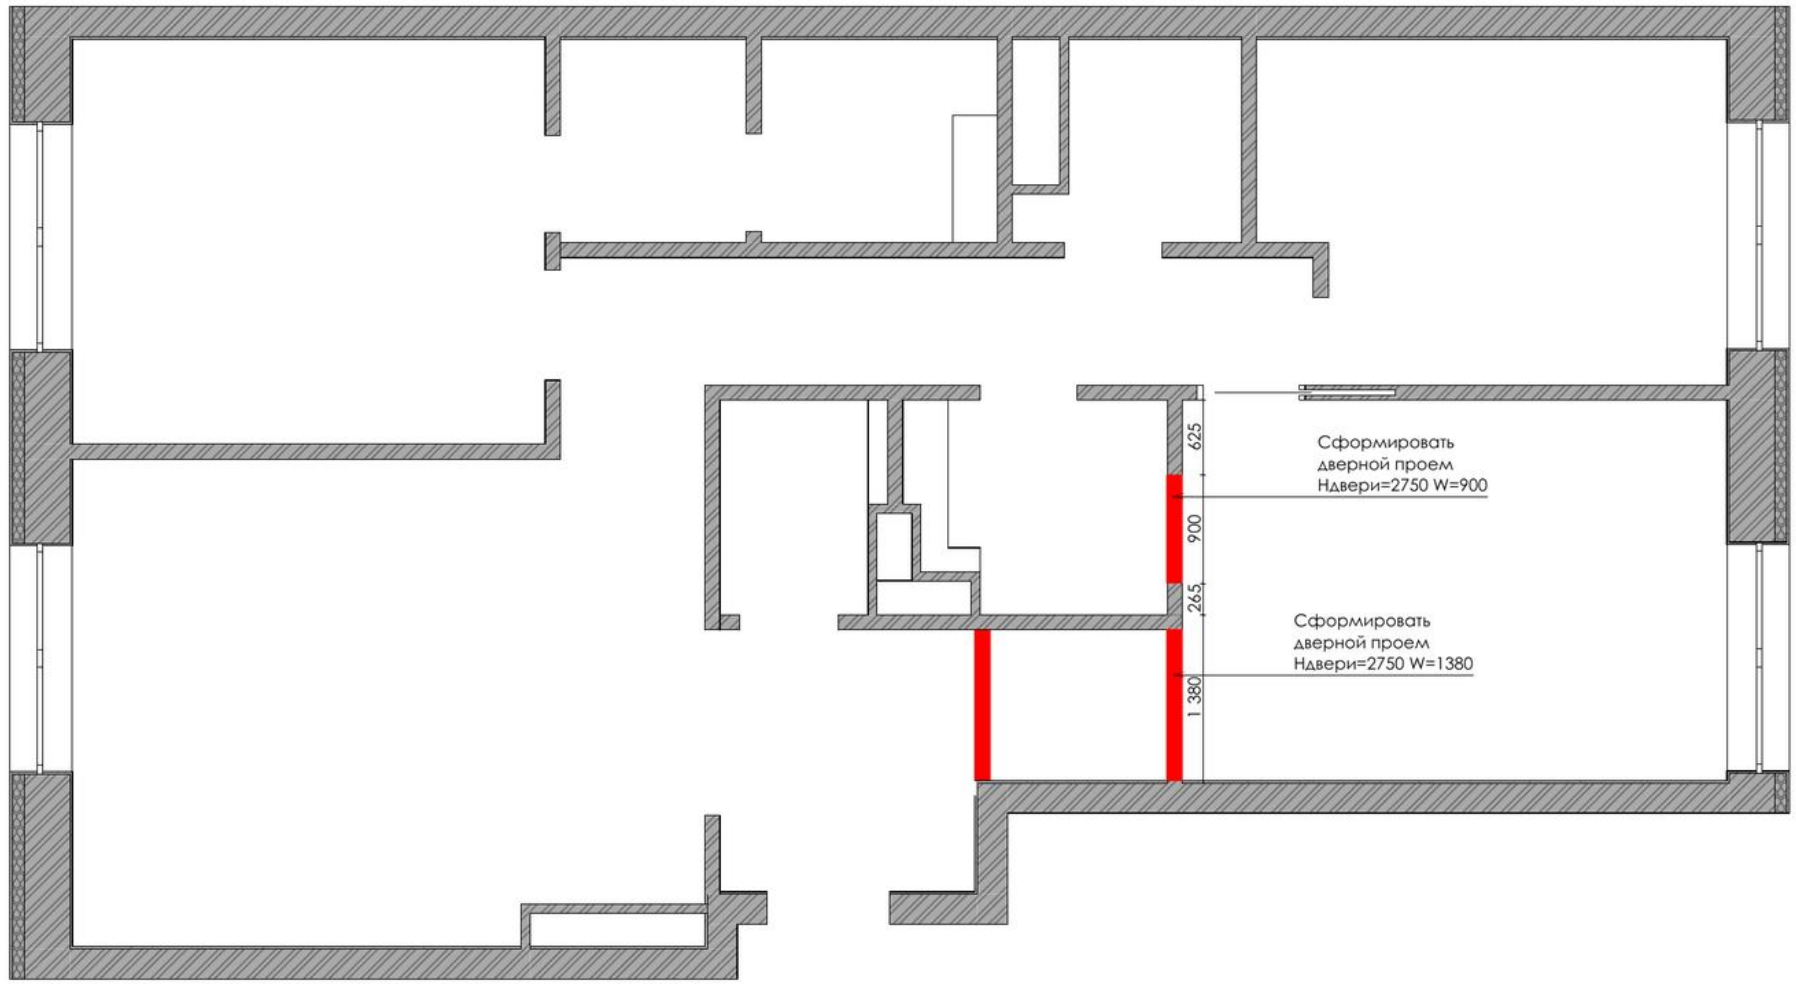


УСЛОВНЫЕ ОБОЗНАЧЕНИЯ

- Демонтируемые стены

- Основные стены

Чертежник:	Курманалиева	Малика		г. Москва	Стадия	Лист	Листов
Визуализатор:	Маматибраимова	Амина			#Стадия Проекта	04	
				Демонтажный план			

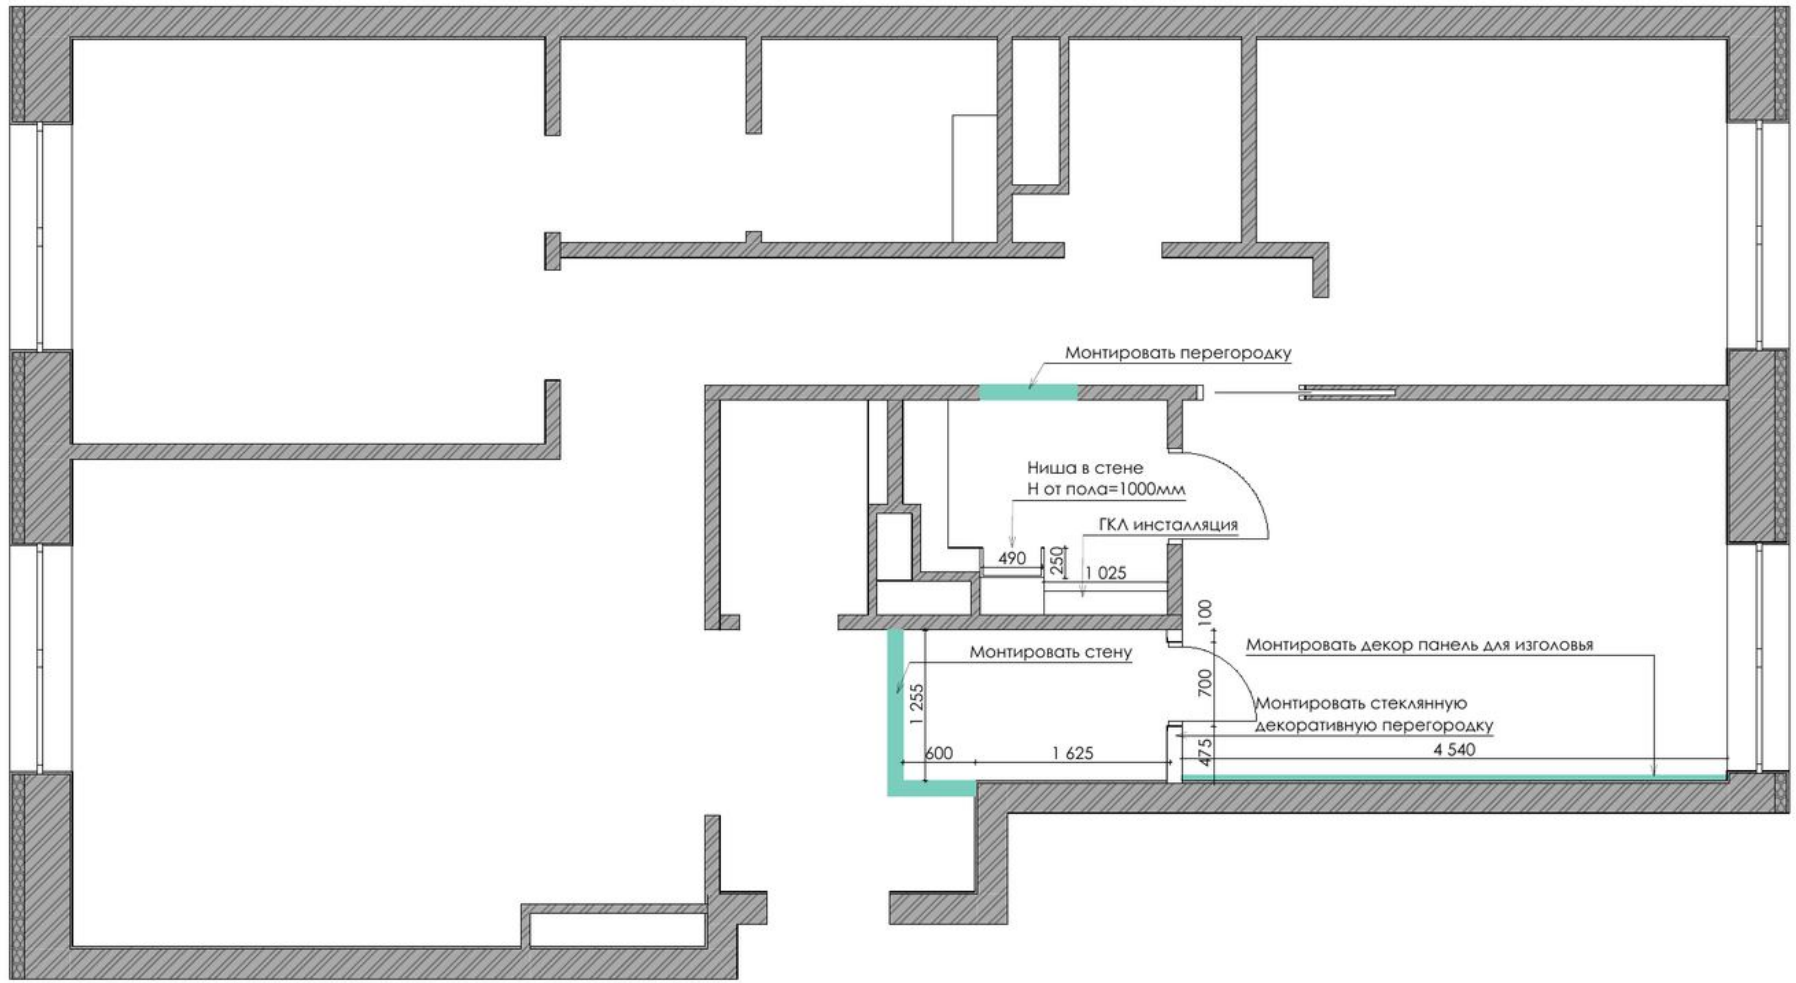


УСЛОВНЫЕ ОБОЗНАЧЕНИЯ

- Демонтируемые стены


- Основные стены

Чертежник:	Курманалиева	Малика		г. Москва	Стадия	Лист	Листов
Визуализатор:	Маматибраимова	Амина			#Стадия Проекта	05	
				Монтажный план			

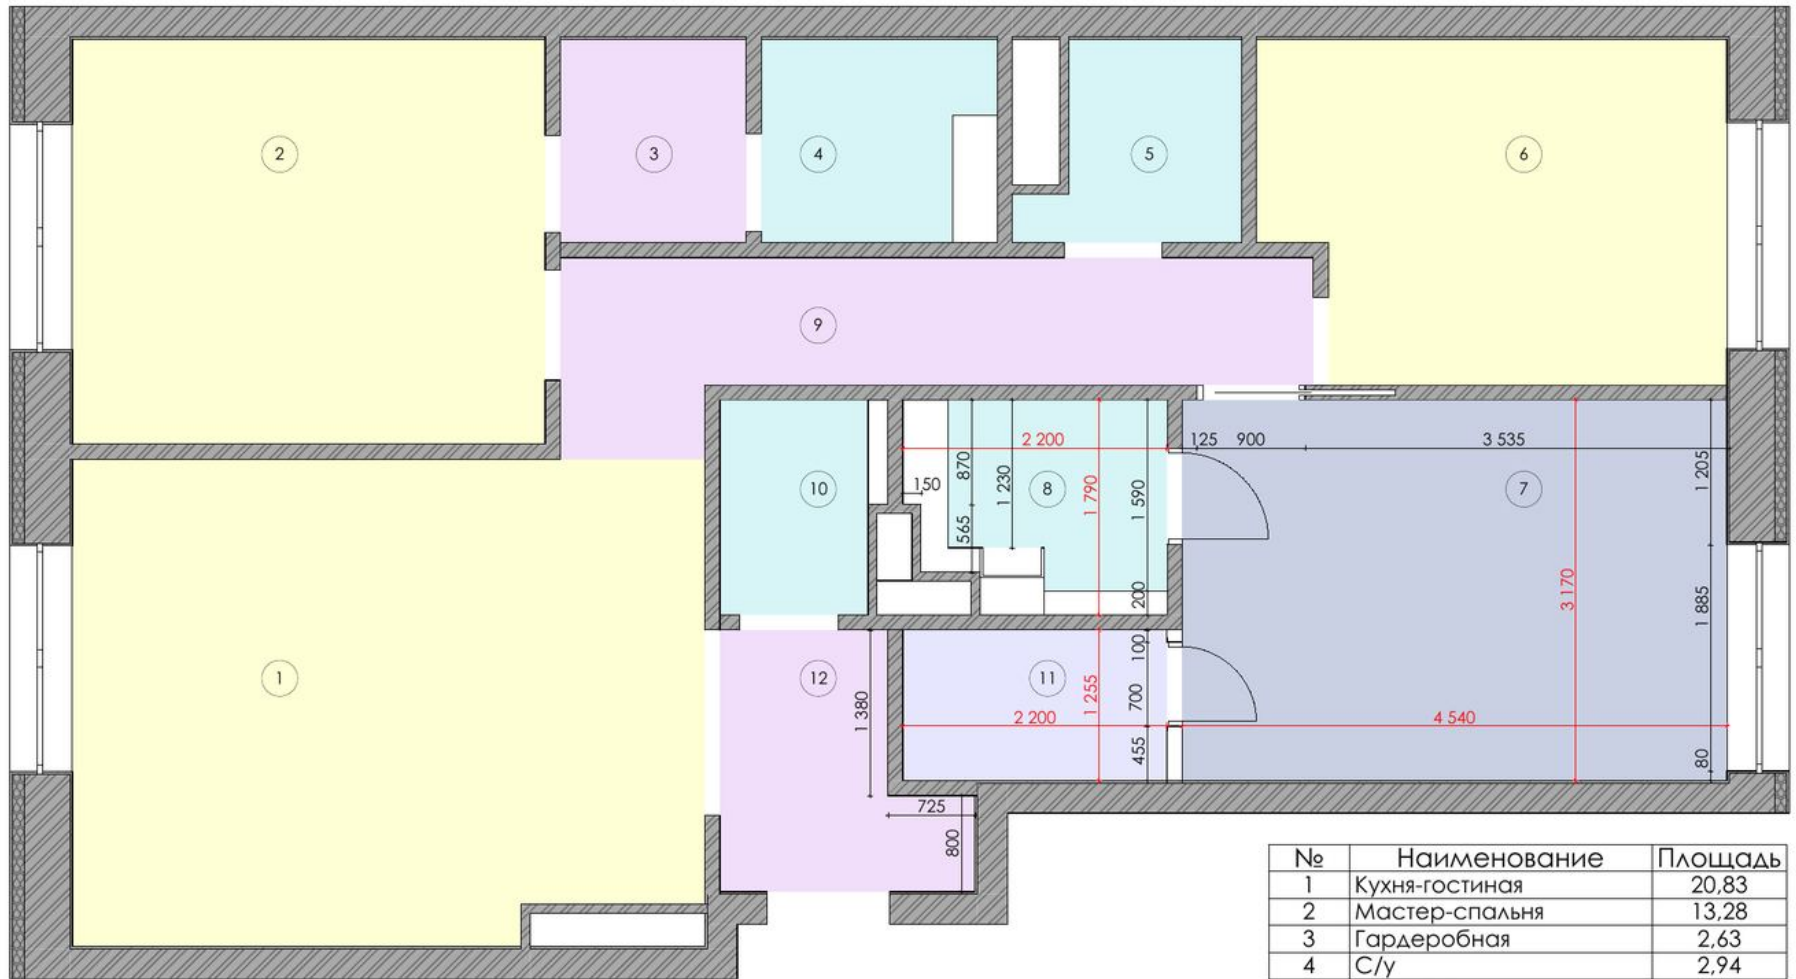


№	Наименование	Площадь
1	Кухня-гостиная	20,83
2	Мастер-спальня	13,28
3	Гардеробная	2,63
4	С/у	2,94
5	Постирочная	2,63
6	Комната	10,58
7	С/у	14,39
8	С/у	2,61
9	Коридор	7,40
10	С/у гостевой	2,21
11	С/у	2,76
12	Прихожая	3,63
		85,89 м²

Чертежник:	Курманалиева	Малика		г. Москва	Стадия	Лист	Листов
Визуализатор:	Маматибраимова	Амина			#Стадия Проекта	06	
				План перепланировки			

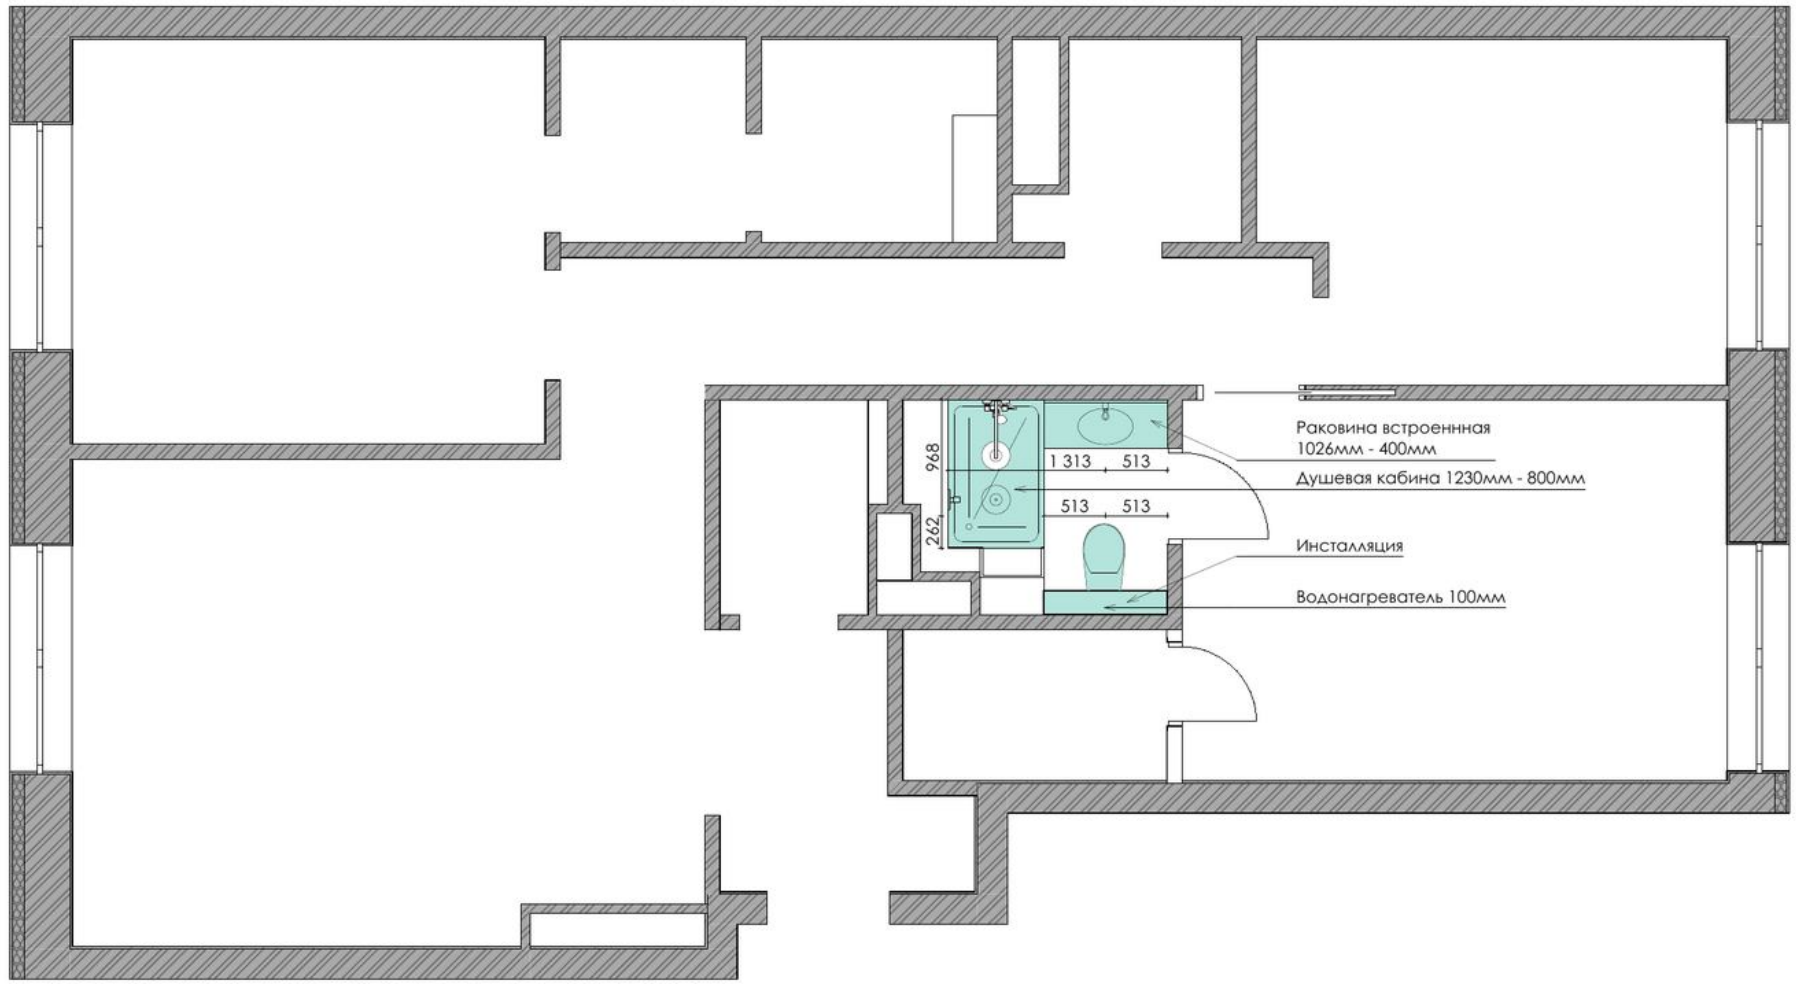

Чертежник:	Курманалиева	Малика		г. Москва	Стадия	Лист	Листов
Визуализатор:	Маматибраимова	Амина			#Стадия Проекта	07	
				План сантехники			

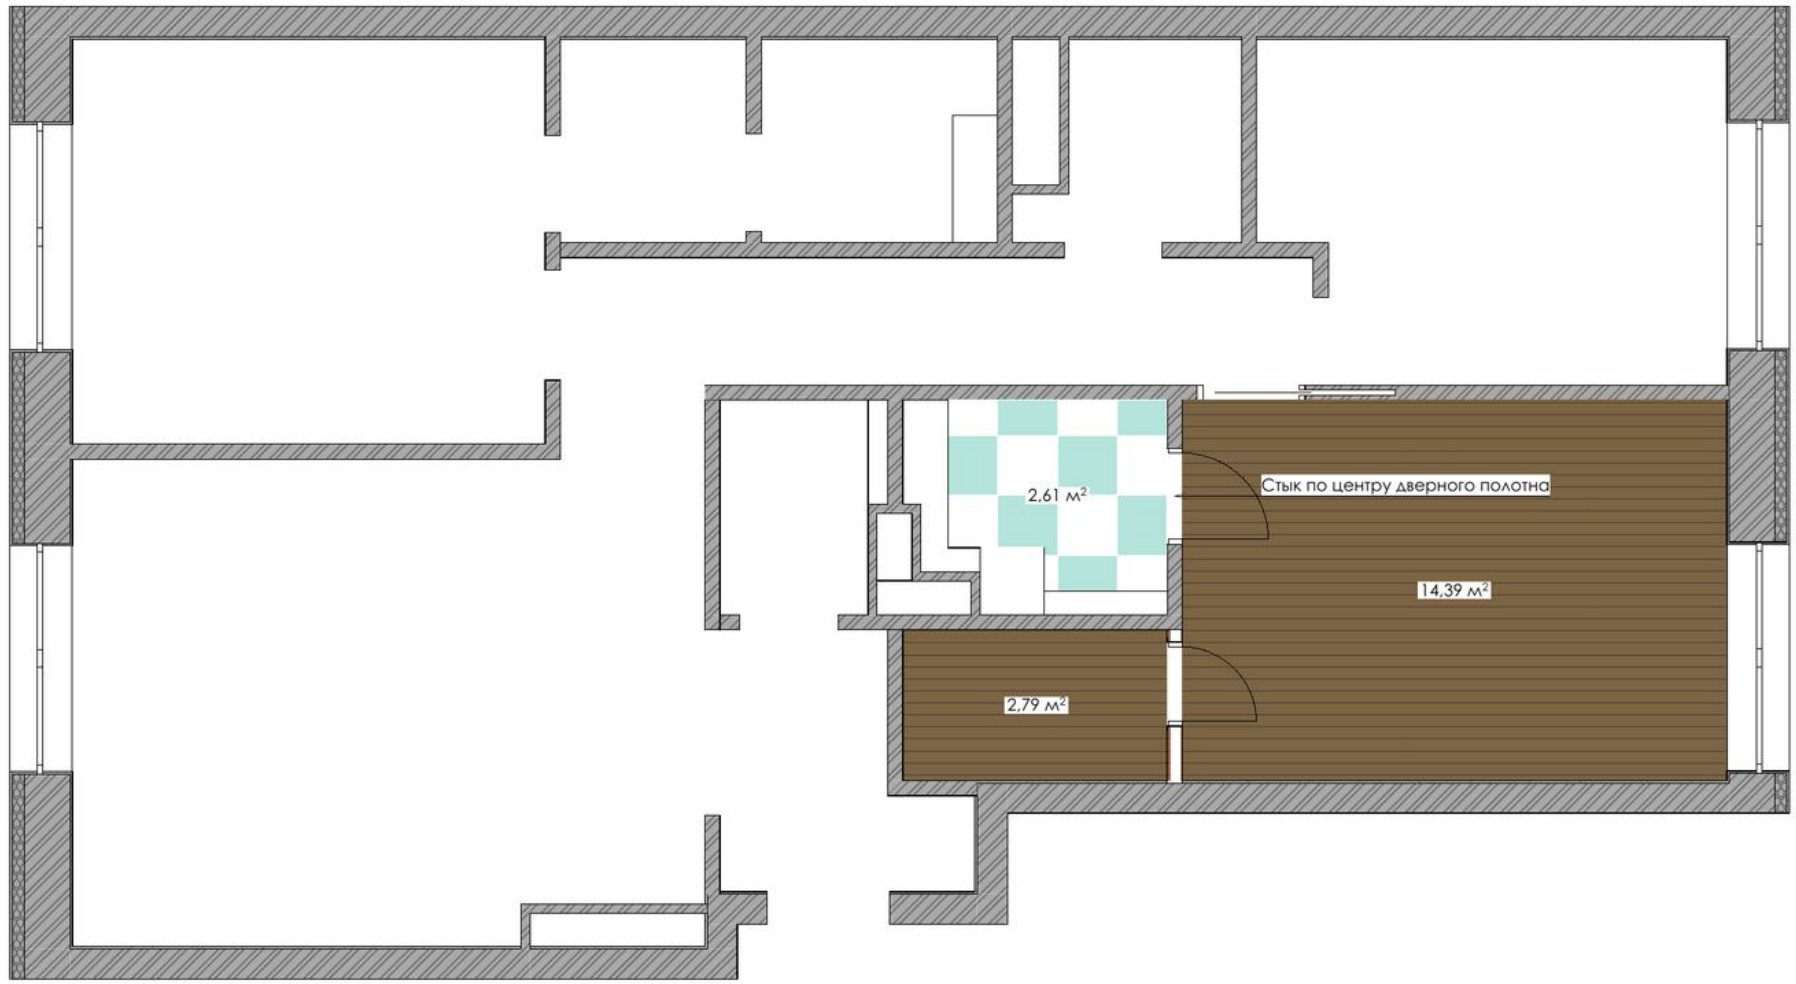


УСЛОВНЫЕ ОБОЗНАЧЕНИЯ

- Ламинат 17,18 (+10%)

- Керамическая плита 3м²

Чертежник:	Курманалиева	Малика		г. Москва	Стадия	Лист	Листов
Визуализатор:	Маматибраимова	Амина			#Стадия Проекта	08	
				План напольного покрытия			

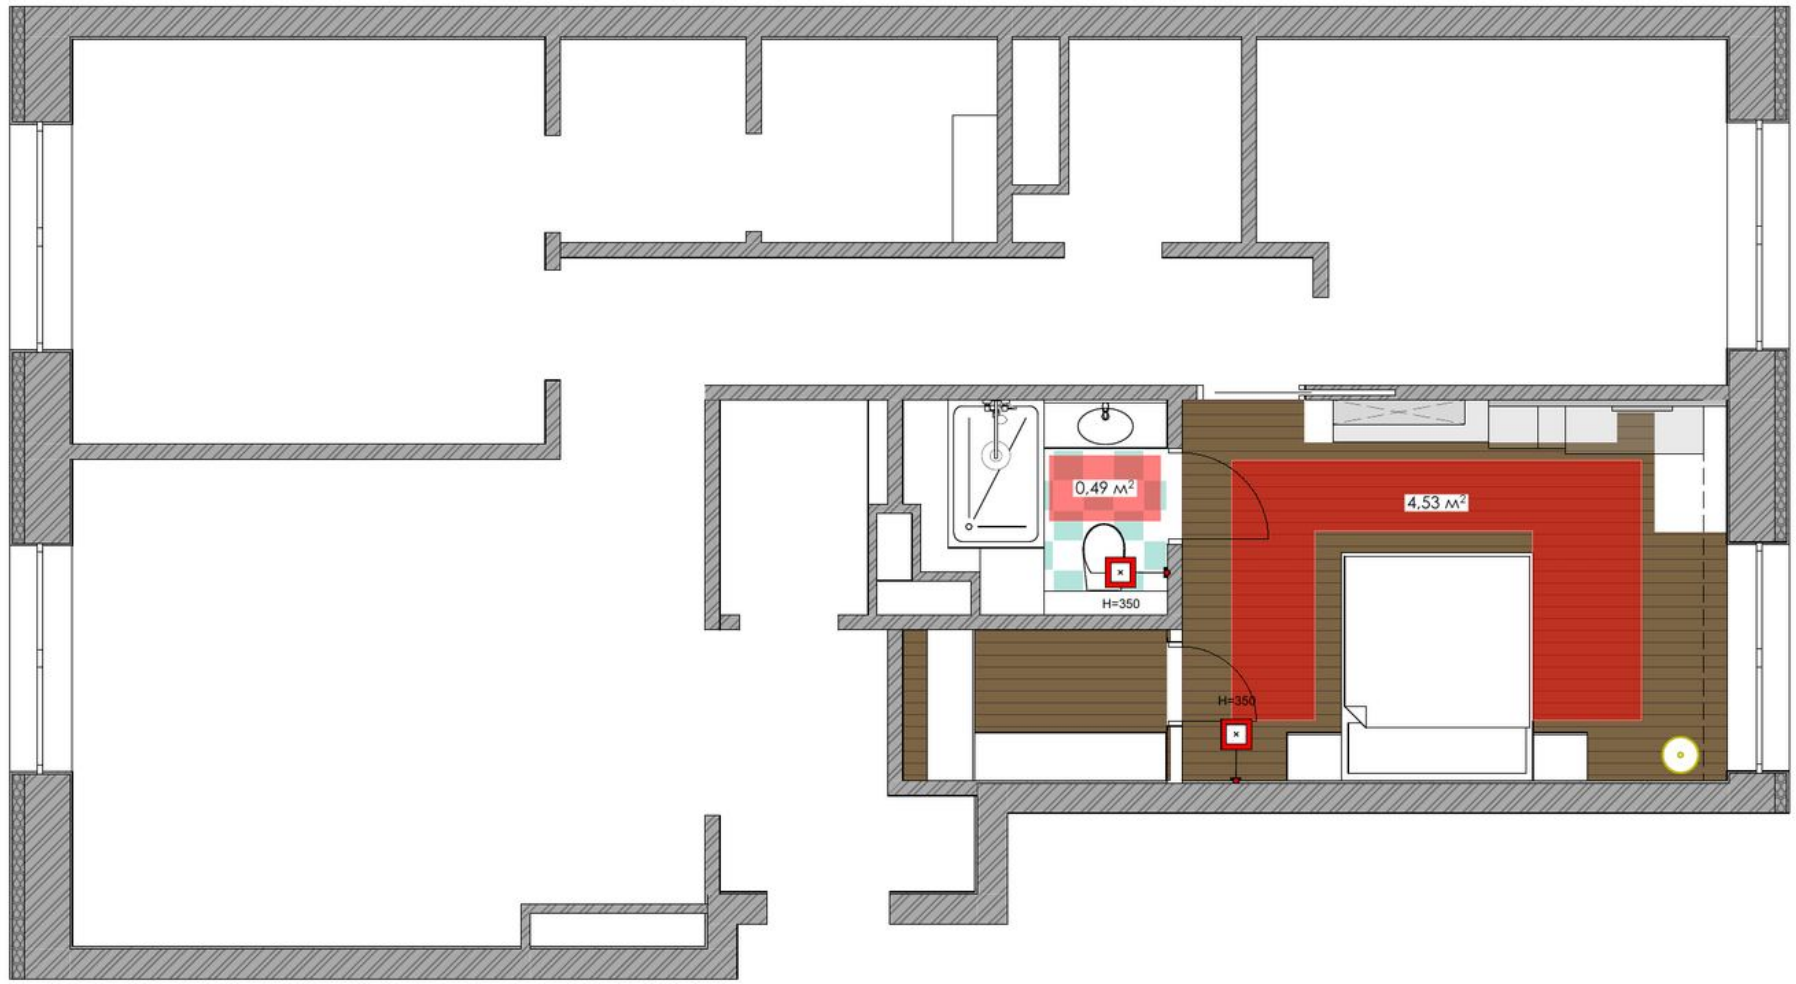


УСЛОВНЫЕ ОБОЗНАЧЕНИЯ

- Теплый пол 5,02м²


- Регулятор ТП 2шт

Чертежник:	Курманалиева	Малика		г. Москва	Стадия	Лист	Листов
Визуализатор:	Маматибраимова	Амина			#Стадия Проекта	09	
				План теплого пола			

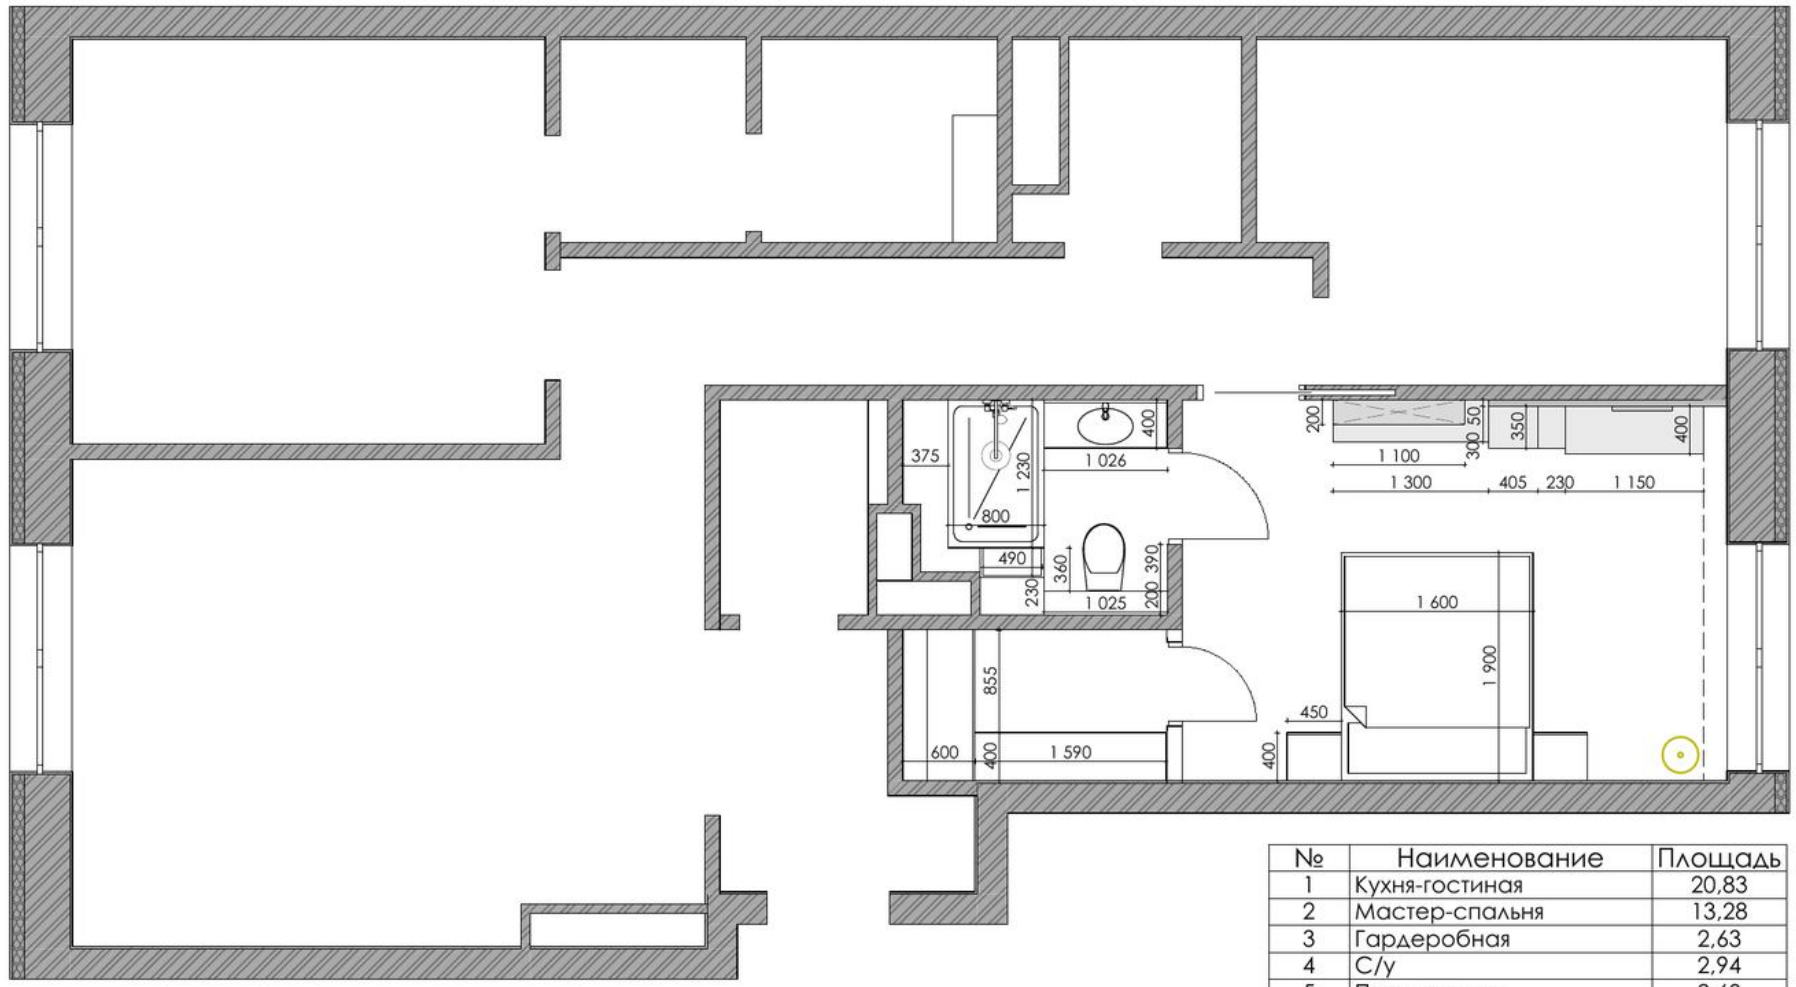


№	Наименование	Площадь
1	Кухня-гостиная	20,83
2	Мастер-спальня	13,28
3	Гардеробная	2,63
4	С/у	2,94
5	Постирочная	2,63
6	Комната	10,58
7	С/у	14,39
8	С/у	2,61
9	Коридор	7,40
10	С/у гостевой	2,21
11	С/у	2,76
12	Прихожая	3,63
		85,89 м²

Чертежник:	Курманалиева	Малика		г. Москва	Стадия	Лист	Листов
Визуализатор:	Маматибраимова	Амина			#Стадия Проекта	10	
				План мебели			

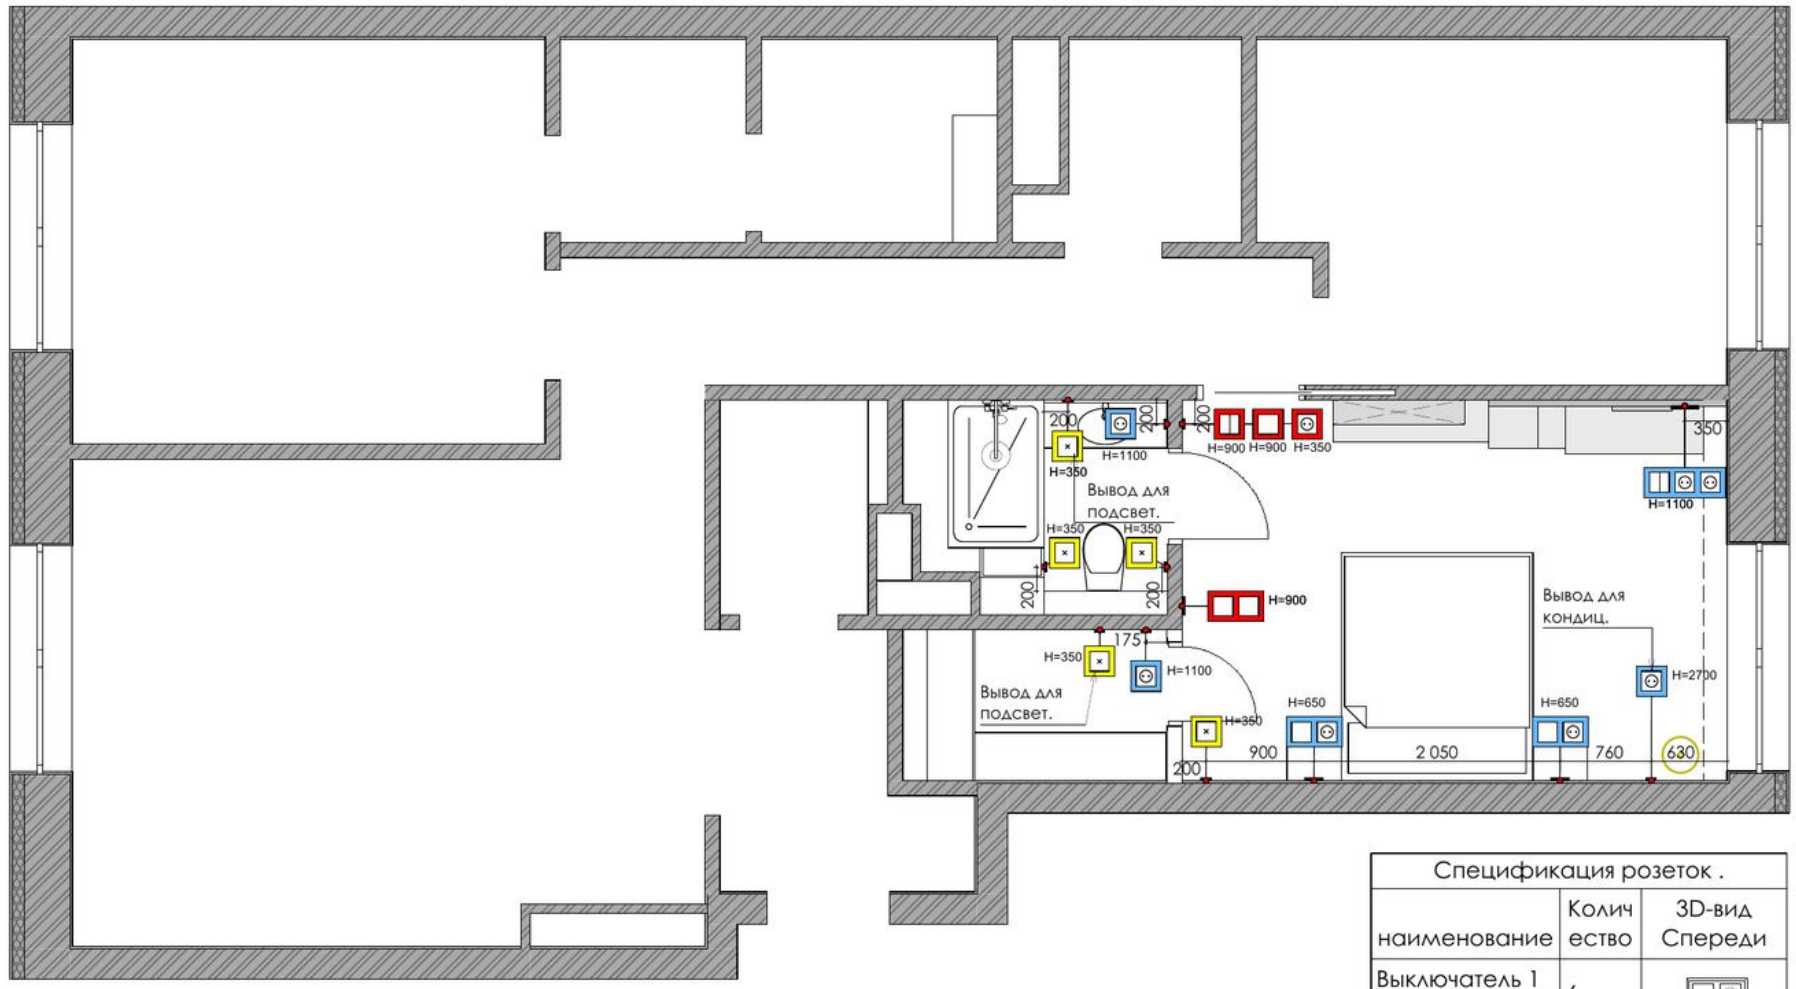


Спецификация розеток .		
наименование	Количество	3D-вид Спереди
Выключатель 1 клавишный	6	
Выключатель 2 клавишный	1	
Подсветка	1	
Розетка 220V	4	
	12	

Чертежник:	Курманалиева	Малика		г. Москва	Стадия	Лист	Листов
Визуализатор:	Маматибраимова	Амина			#Стадия Проекта	11	
				План розеточных групп			

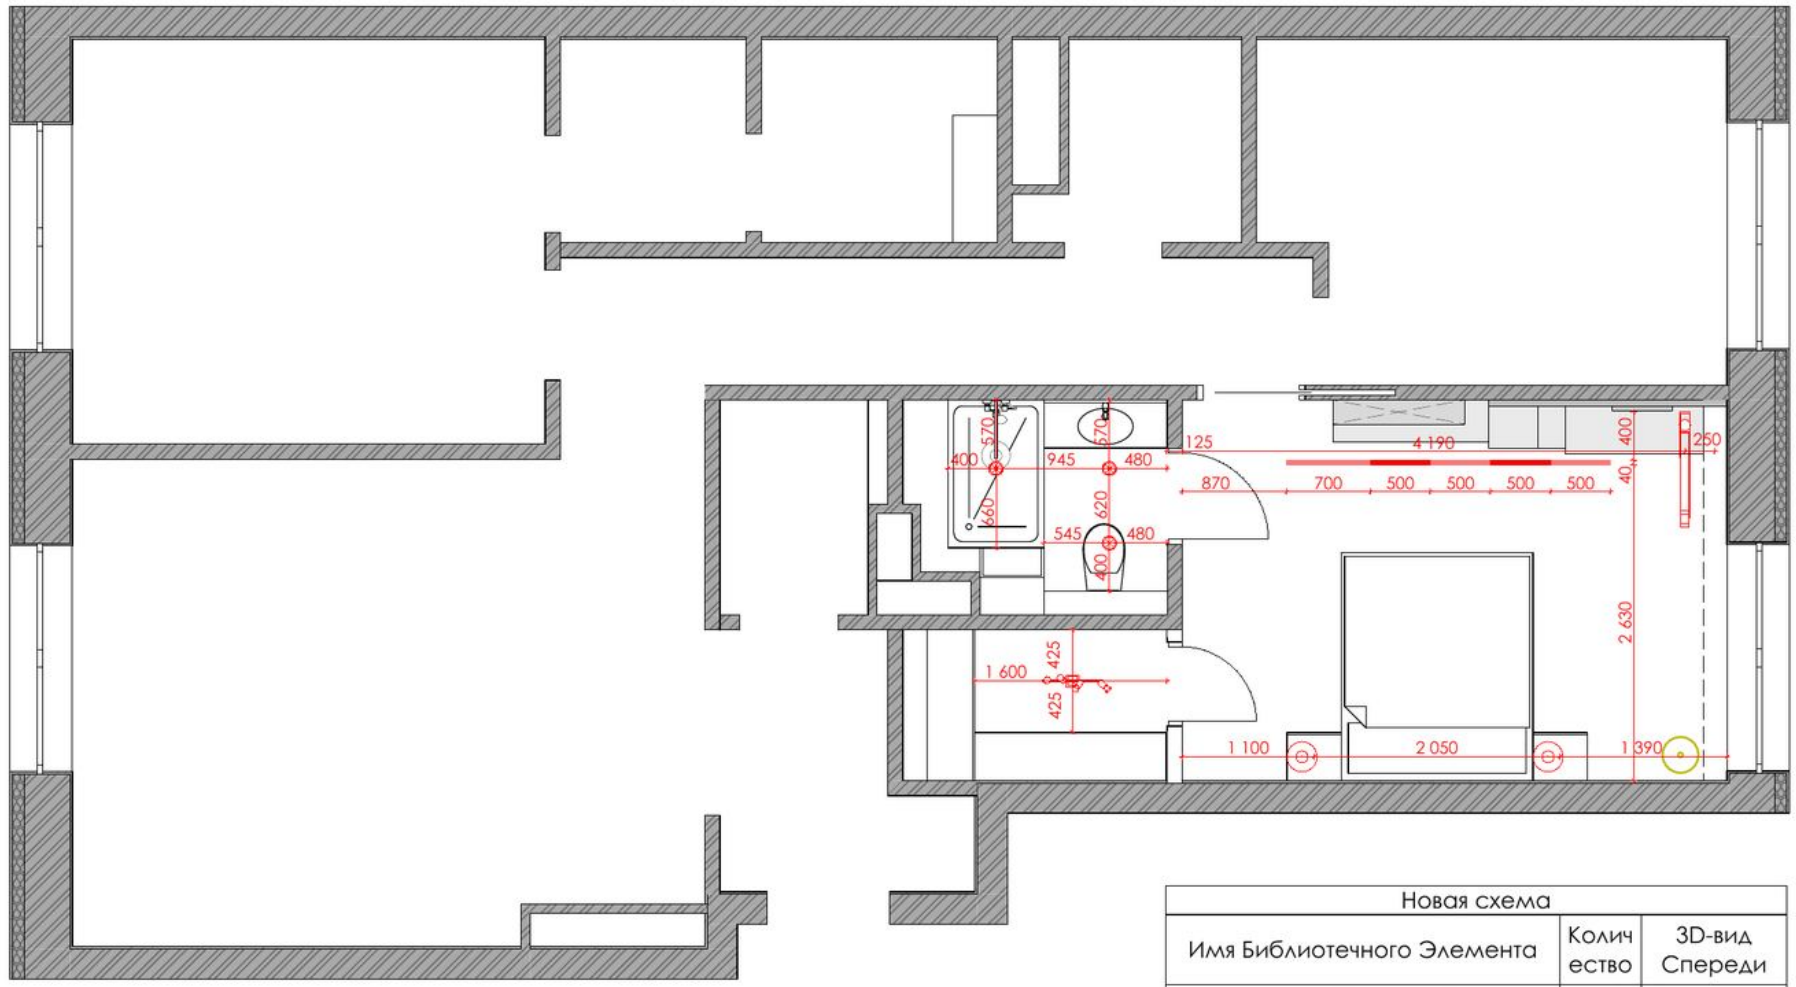


Новая схема		
Имя Библиотечного Элемента	Количество	3D-вид Спереди
Встраиваемый Точечный Светильник 26	3	
Набор Источников Света Потолочный 26	3	
Подвесной Светильник 26	2	
	8	

Чертежник:	Курманалиева	Малика		г. Москва	Стадия	Лист	Листов
Визуализатор:	Маматибраимова	Амина			#Стадия Проекта	12	
				План осветительных приборов			

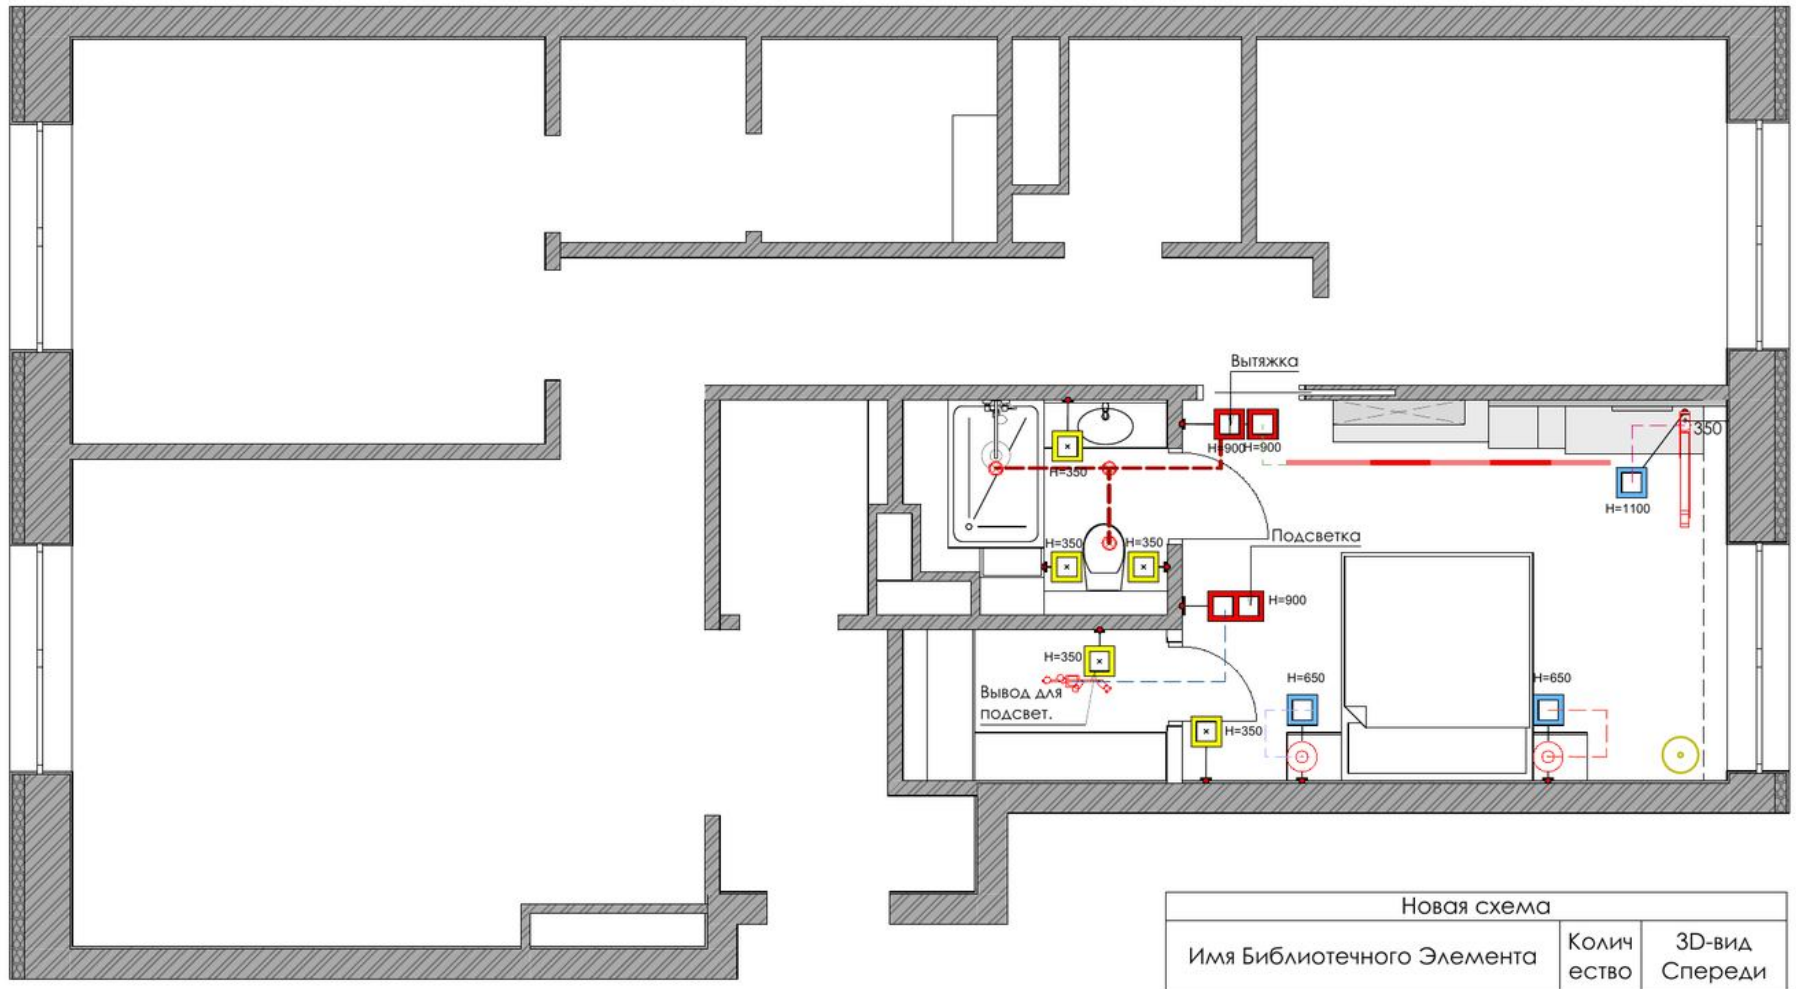

Новая схема		
Имя Библиотечного Элемента	Количество	3D-вид Спереди
Встраиваемый Точечный Светильник 26	3	
Набор Источников Света Потолочный 26	3	
Подвесной Светильник 26	2	
	8	


Чертежник:	Курманалиева	Малика		г. Москва	Стадия	Лист	Листов
Визуализатор:	Маматибраимова	Амина			#Стадия Проекта	13	
				План освещения			

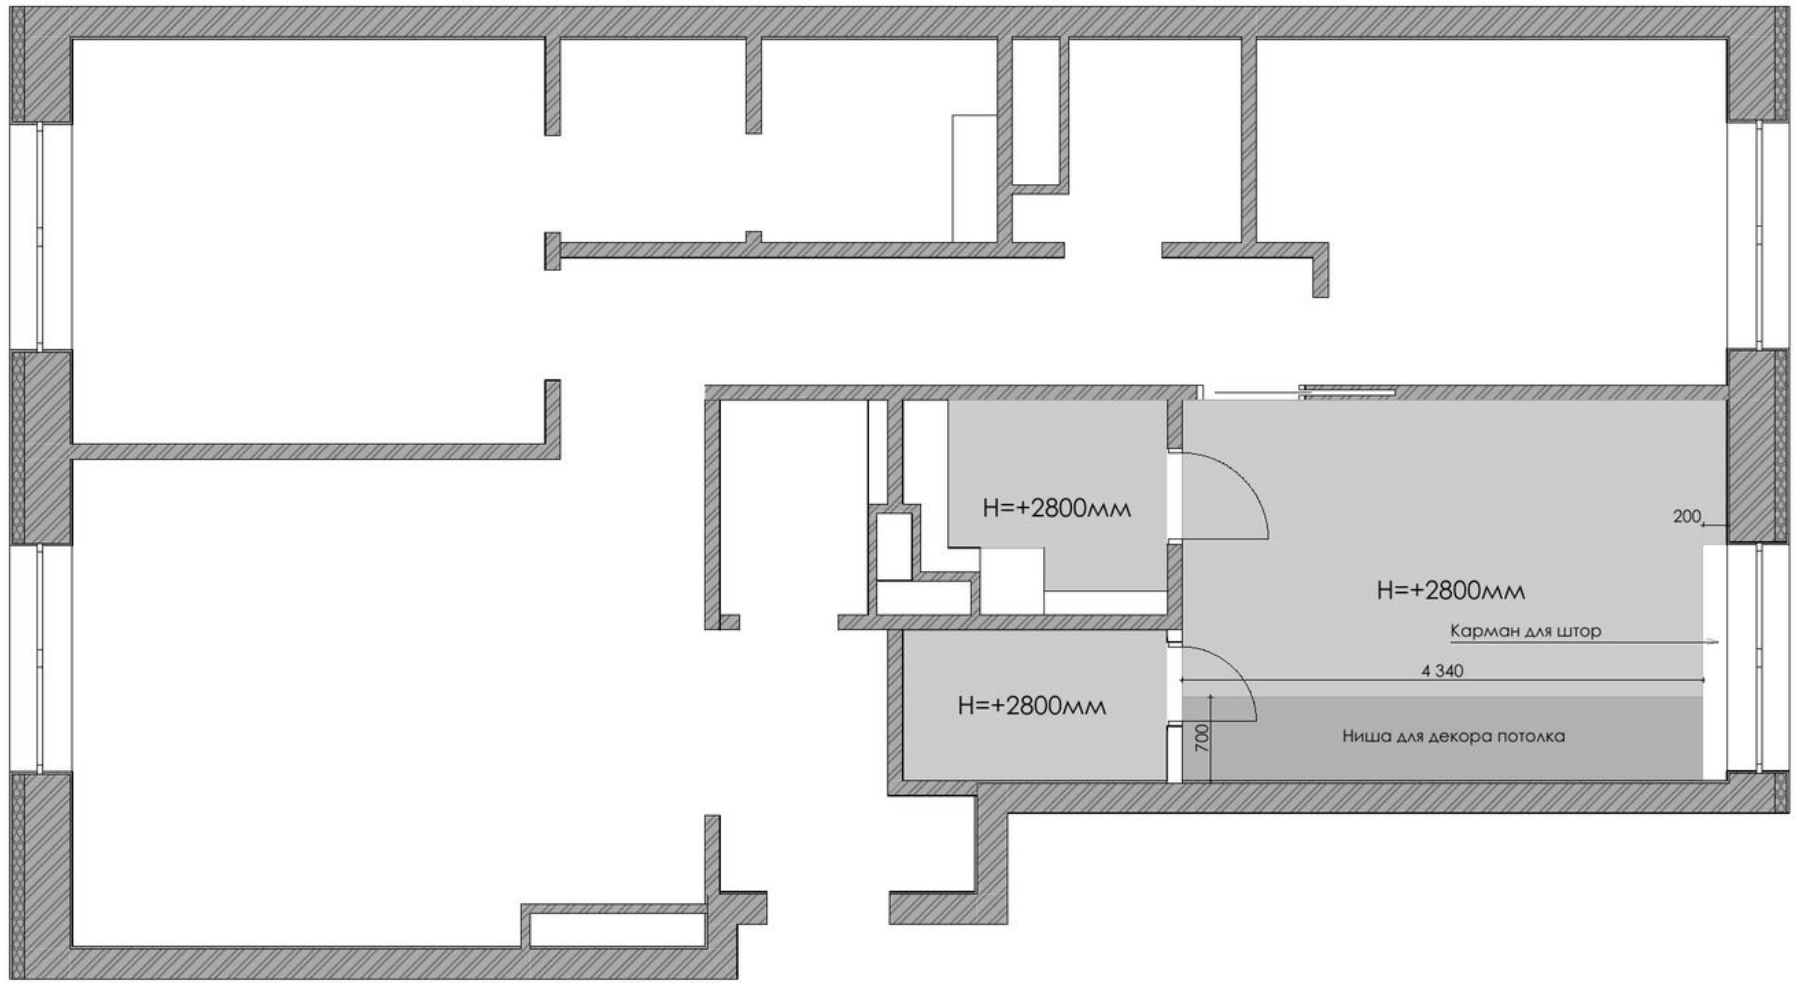

УСЛОВНЫЕ ОБОЗНАЧЕНИЯ


- ГКЛ потолок


Чертежник:	Курманалиева	Малика		г. Москва	Стадия	Лист	Листов
Визуализатор:	Маматибраимова	Амина			#Стадия Проекта	14	
				План потолка			

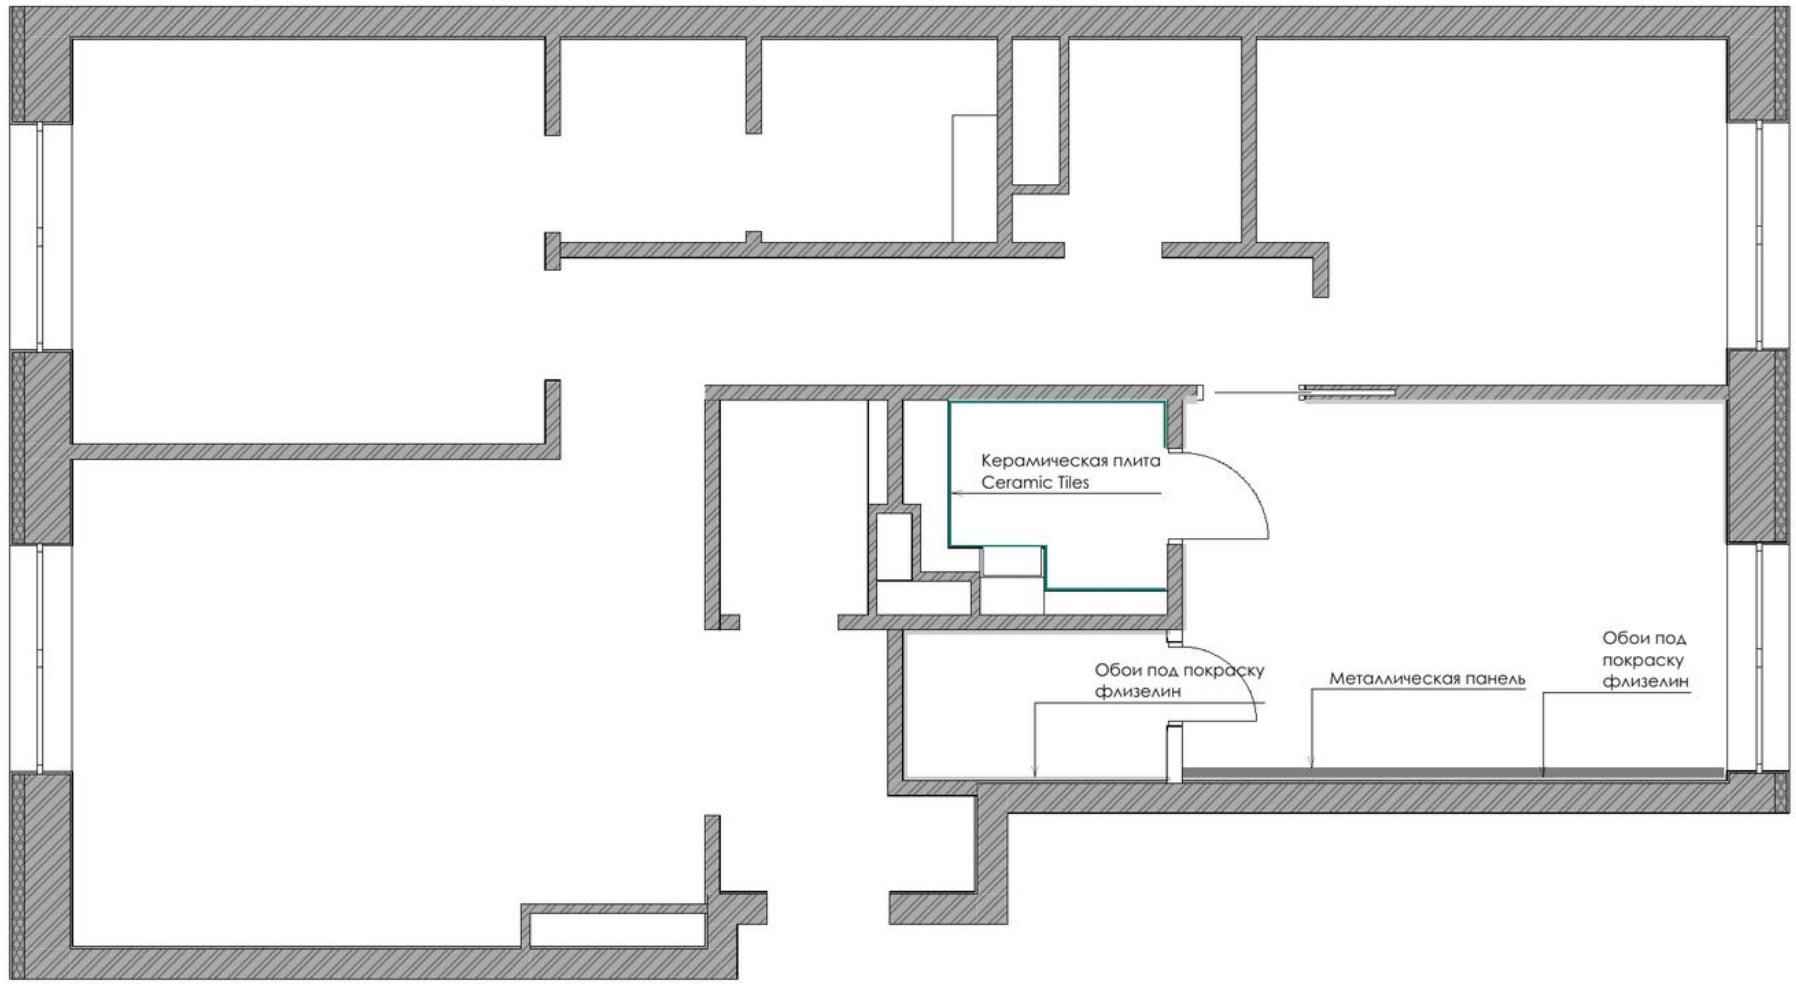



Отделка стен		
Вид на плане	Покрытие	S, м^2
	Обои под покраску, флизелин	0,50м^2
	Металлическая панель	0,36м^2
	Керамическая плита	0,17м^2

Чертежник:	Курманалиева	Малика		г. Москва	Стадия	Лист	Листов
Визуализатор:	Маматибраимова	Амина			#Стадия Проекта	15	
				План отделки стен			

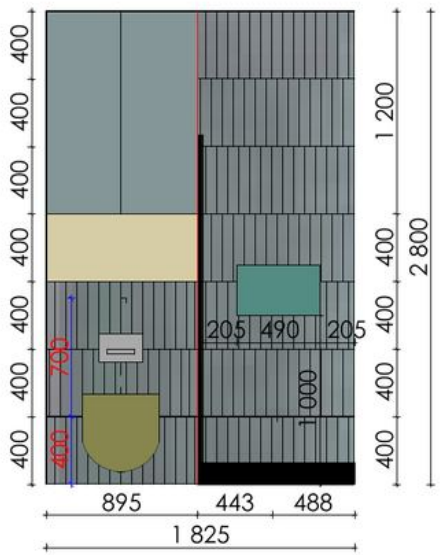

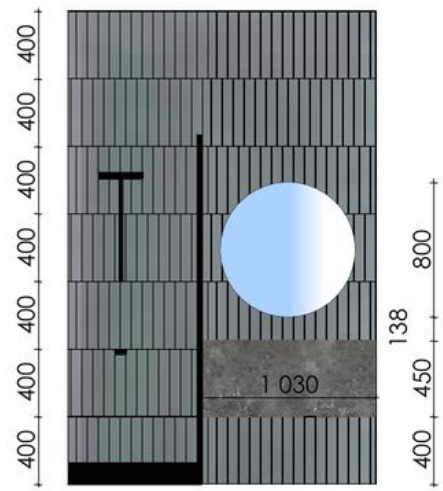


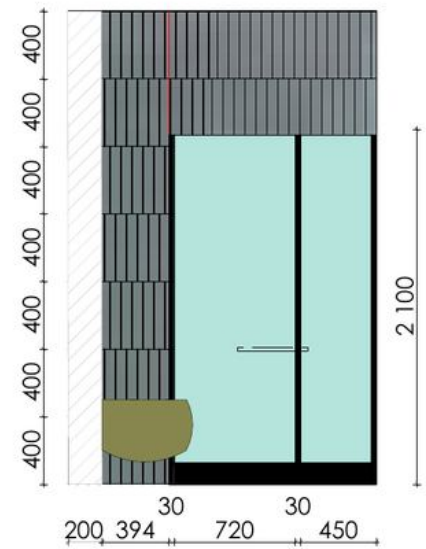

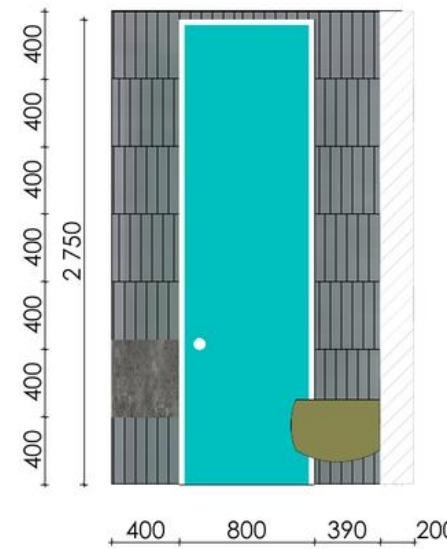


Чертежник:	Курманалиева	Малика		г. Москва	Стадия	Лист	Листов
Визуализатор:	Маматибраимова	Амина			#Стадия Проекта	16	
				Развертки санузла			


Вид сверху

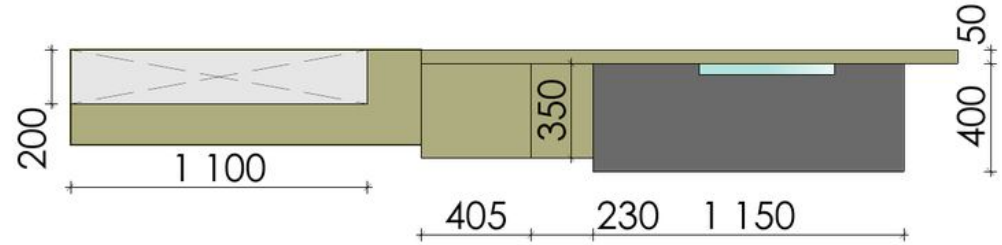

Вид спереди

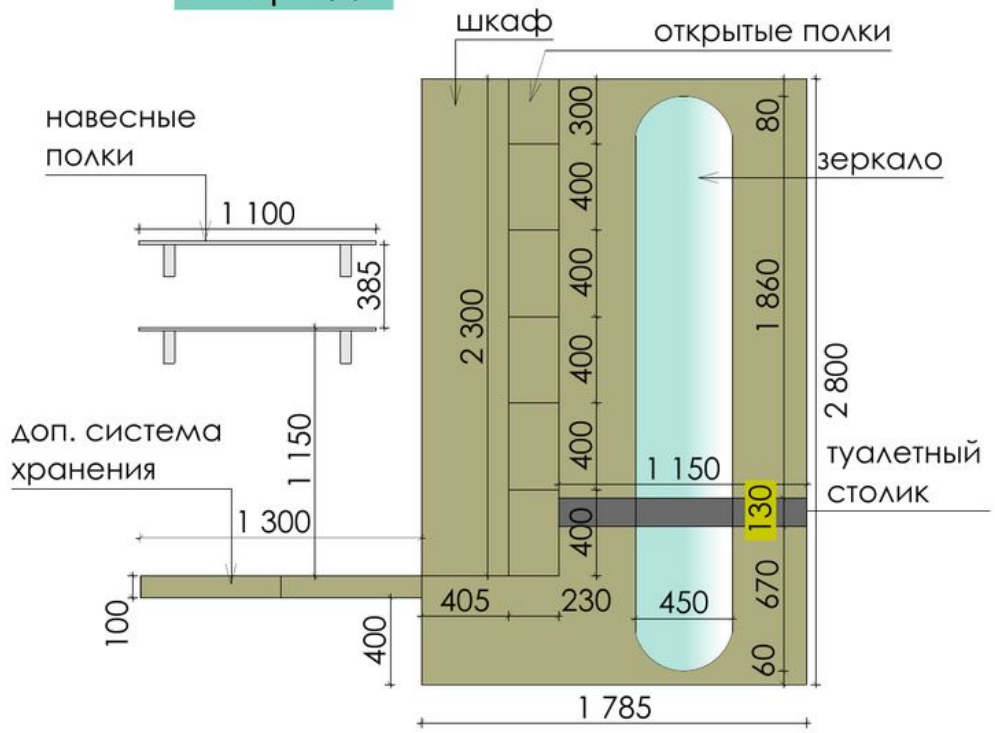


Вид сбоку

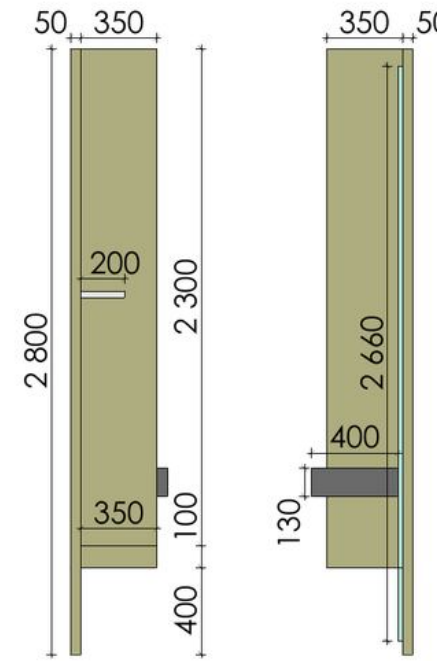


Чертежник:	Курманалиева	Малика		г. Москва	Стадия	Лист	Листов
Визуализатор:	Маматибраимова	Амина			#Стадия Проекта	17	
				Спецификация мебели			


Вид спереди

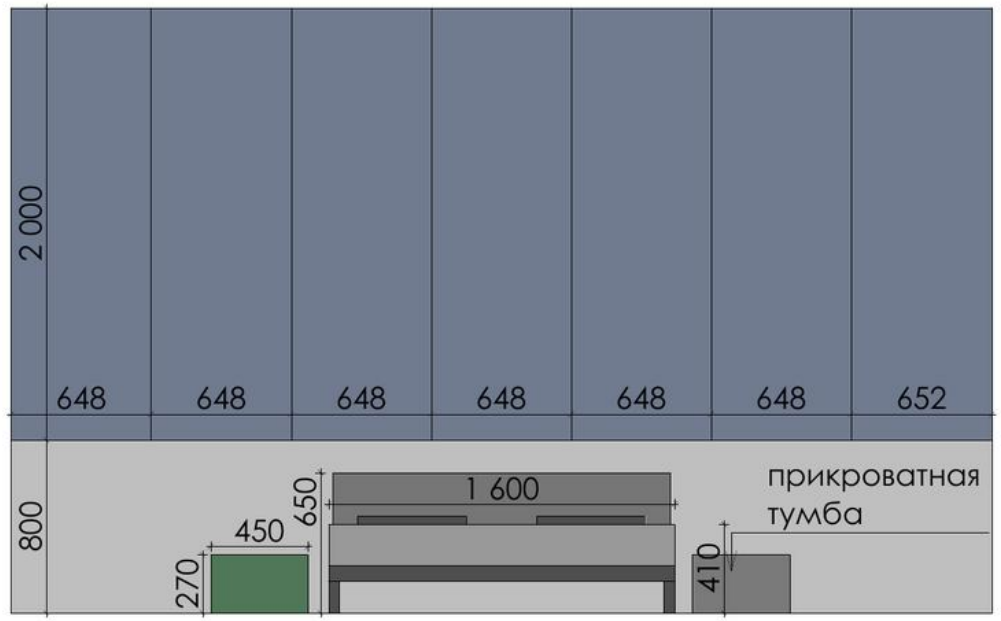

Вид сбоку

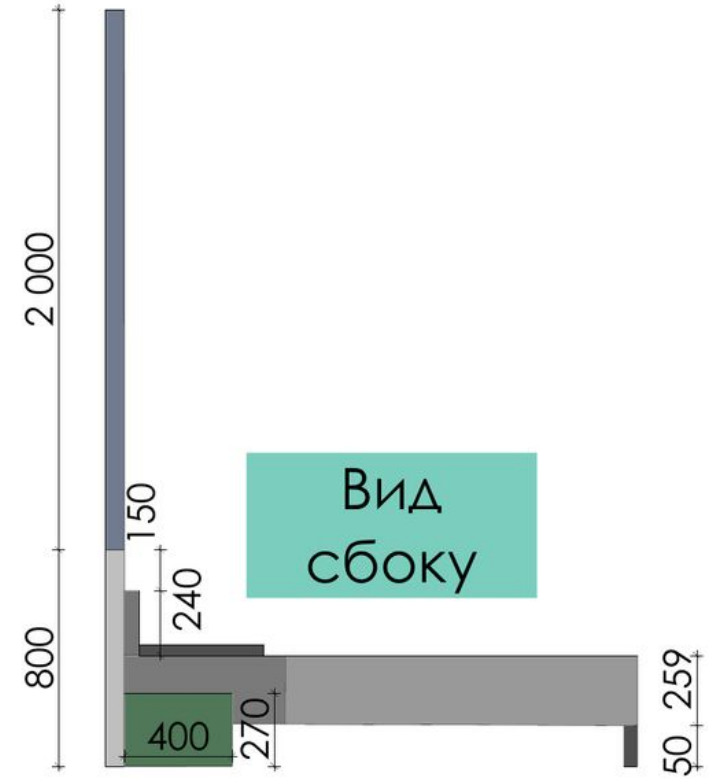



Вид сверху

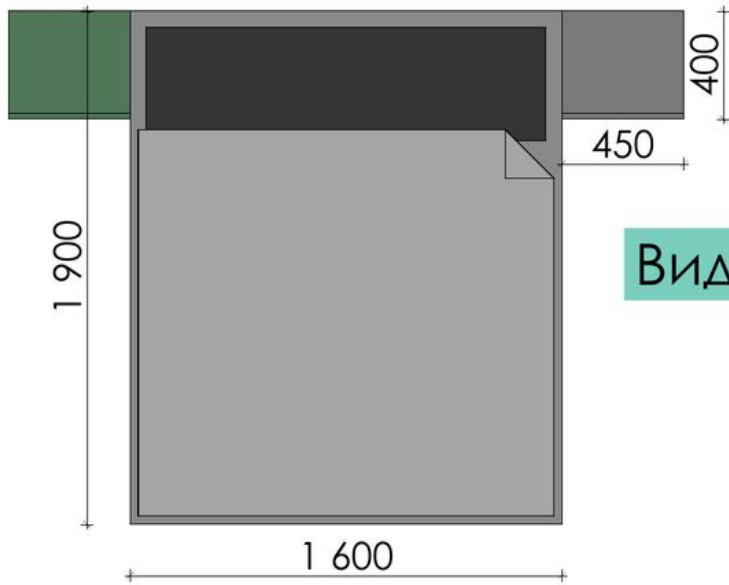


Чертежник:	Курманалиева	Малика		г. Москва	Стадия	Лист	Листов
Визуализатор:	Маматибраимова	Амина			#Стадия Проекта	18	
				Спецификация мебели №2			

Вид сбоку

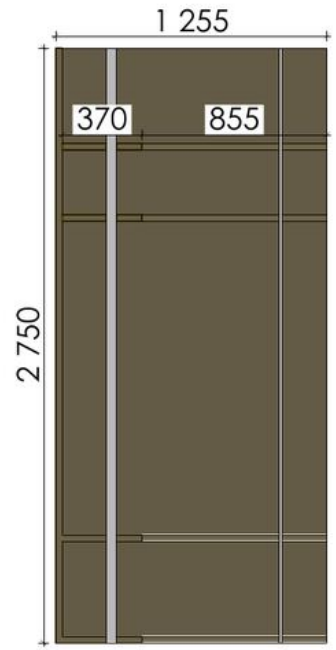

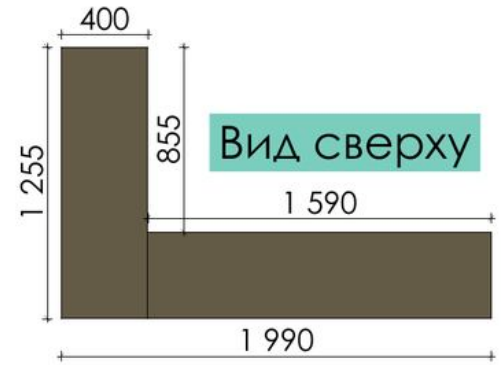

Вид сверху

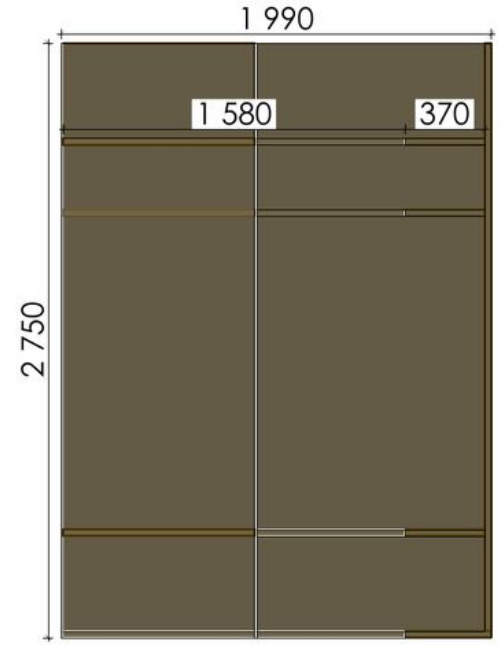

Вид спереди

Чертежник:	Курманалиева	Малика		г. Москва	Стадия	Лист	Листов
Визуализатор:	Маматибраимова	Амина			#Стадия Проекта	19	
				Спецификация мебели №3			